

MIER Y TERÁN GALVANDUQUE®

PROYECTO EJECUTIVO PASTICCIO


BY

MYTELVDK

Creative office for Architecture, Furniture Design
& Brand Identity. Mexico City, Mx.


[MEXICO
CITY
BASED

LISTADO DE CONTROLES						
CONTROL	APAGADO POR	AREA	ACCESORIO	#	W	TOTAL
24	APAGADOR	Tira LED Marca Neon Flex en área de empleados	-----	2.02 ML	50 W	Pendiente
		Lámpara de sobreponer en área de empleados	○	2	25 W	50 W
25	APAGADOR	Lámpara de sobreponer en área de empleados	○	1	25 W	25 W
26	DIMMER	Cánope lineal en salón de eventos 01	—	5	9 W	45 W
		Arbotante a muro en salón de eventos 01	⌘	7	10 W	70 W
27	DIMMER	Lámpara de suspensión en salón de eventos 01	⊗	1	10 W	10 W
28	DIMMER	Arbotante a muro en salón de eventos 01	⊗	1	10 W	10 W
29	DIMMER	Lámpara de suspensión	⊗	3	10 W	30 W
30	DIMMER	Tira LED Marca Neon Flex	-----	5.45	50 W	Pendiente
31	DIMMER	Lámpara de suspensión en salón de eventos 02	⊗	1	10 W	10 W
32	DIMMER	Cánope lineal en salón de eventos 02	—	10	9 W	90 W
		Arbotante a muro en salón de eventos 02	⌘	10	10 W	100 W
33	DIMMER	Cánope lineal en escalera	—	3	9 W	27 W
		Tira LED Marca Neon Flex en escalera	-----	2.56 ML	50 W	Pendiente
		Caja de luz en escalera	⌘	3	50 W	Pendiente
		Arbotante a muro en escalera	⊗	1	10 W	10 W
34	DIMMER	Proyector a riel en escalera	⌘	12	13 W	156W
35	DIMMER	Tira LED Marca Neon Flex en baños	-----	3.54 ML	50 W	Pendiente
		Lámpara de suspensión en baños	⊗	1	10 W	10 W
36	DIMMER	Arbotante a muro en hall	⊗	1	10 W	10 W
		Caja de luz en hall	⌘	1	50 W	Pendiente
		Tira LED Marca Neon Flex en hall	-----	2.90 ML	50 W	Pendiente
37	DIMMER	Tira LED Marca Neon Flex en barra	-----	2.02 ML	50 W	Pendiente
38	DIMMER	Lámpara de suspensión en barra	⊗	1	10 W	10 W
39	DIMMER	Lámpara de suspensión en cocina	⊗	2	50 W	100 W
40	APAGADOR	Integrada a campanas	⊗	1	Pendiente	Pendiente
41	DIMMER	Arbotante a muro en salon de eventos 03	⊗	9	10 W	90 W
		Arbotante a muro en salón de eventos 03	⌘	2	10 W	20 W
42	DIMMER	Proyector a riel en salón de eventos 03	⌘	14	13 W	182W
		Lámpara de suspensión en salón de eventos 03	⊗	2	10 W	20 W
43	DIMMER	Lámpara de cánope en plafón en salón de eventos 03	○	4	10 W	40 W
44	DIMMER	Lámpara de suspensión en lavado	-----	4.93 ML	50 W	Pendiente

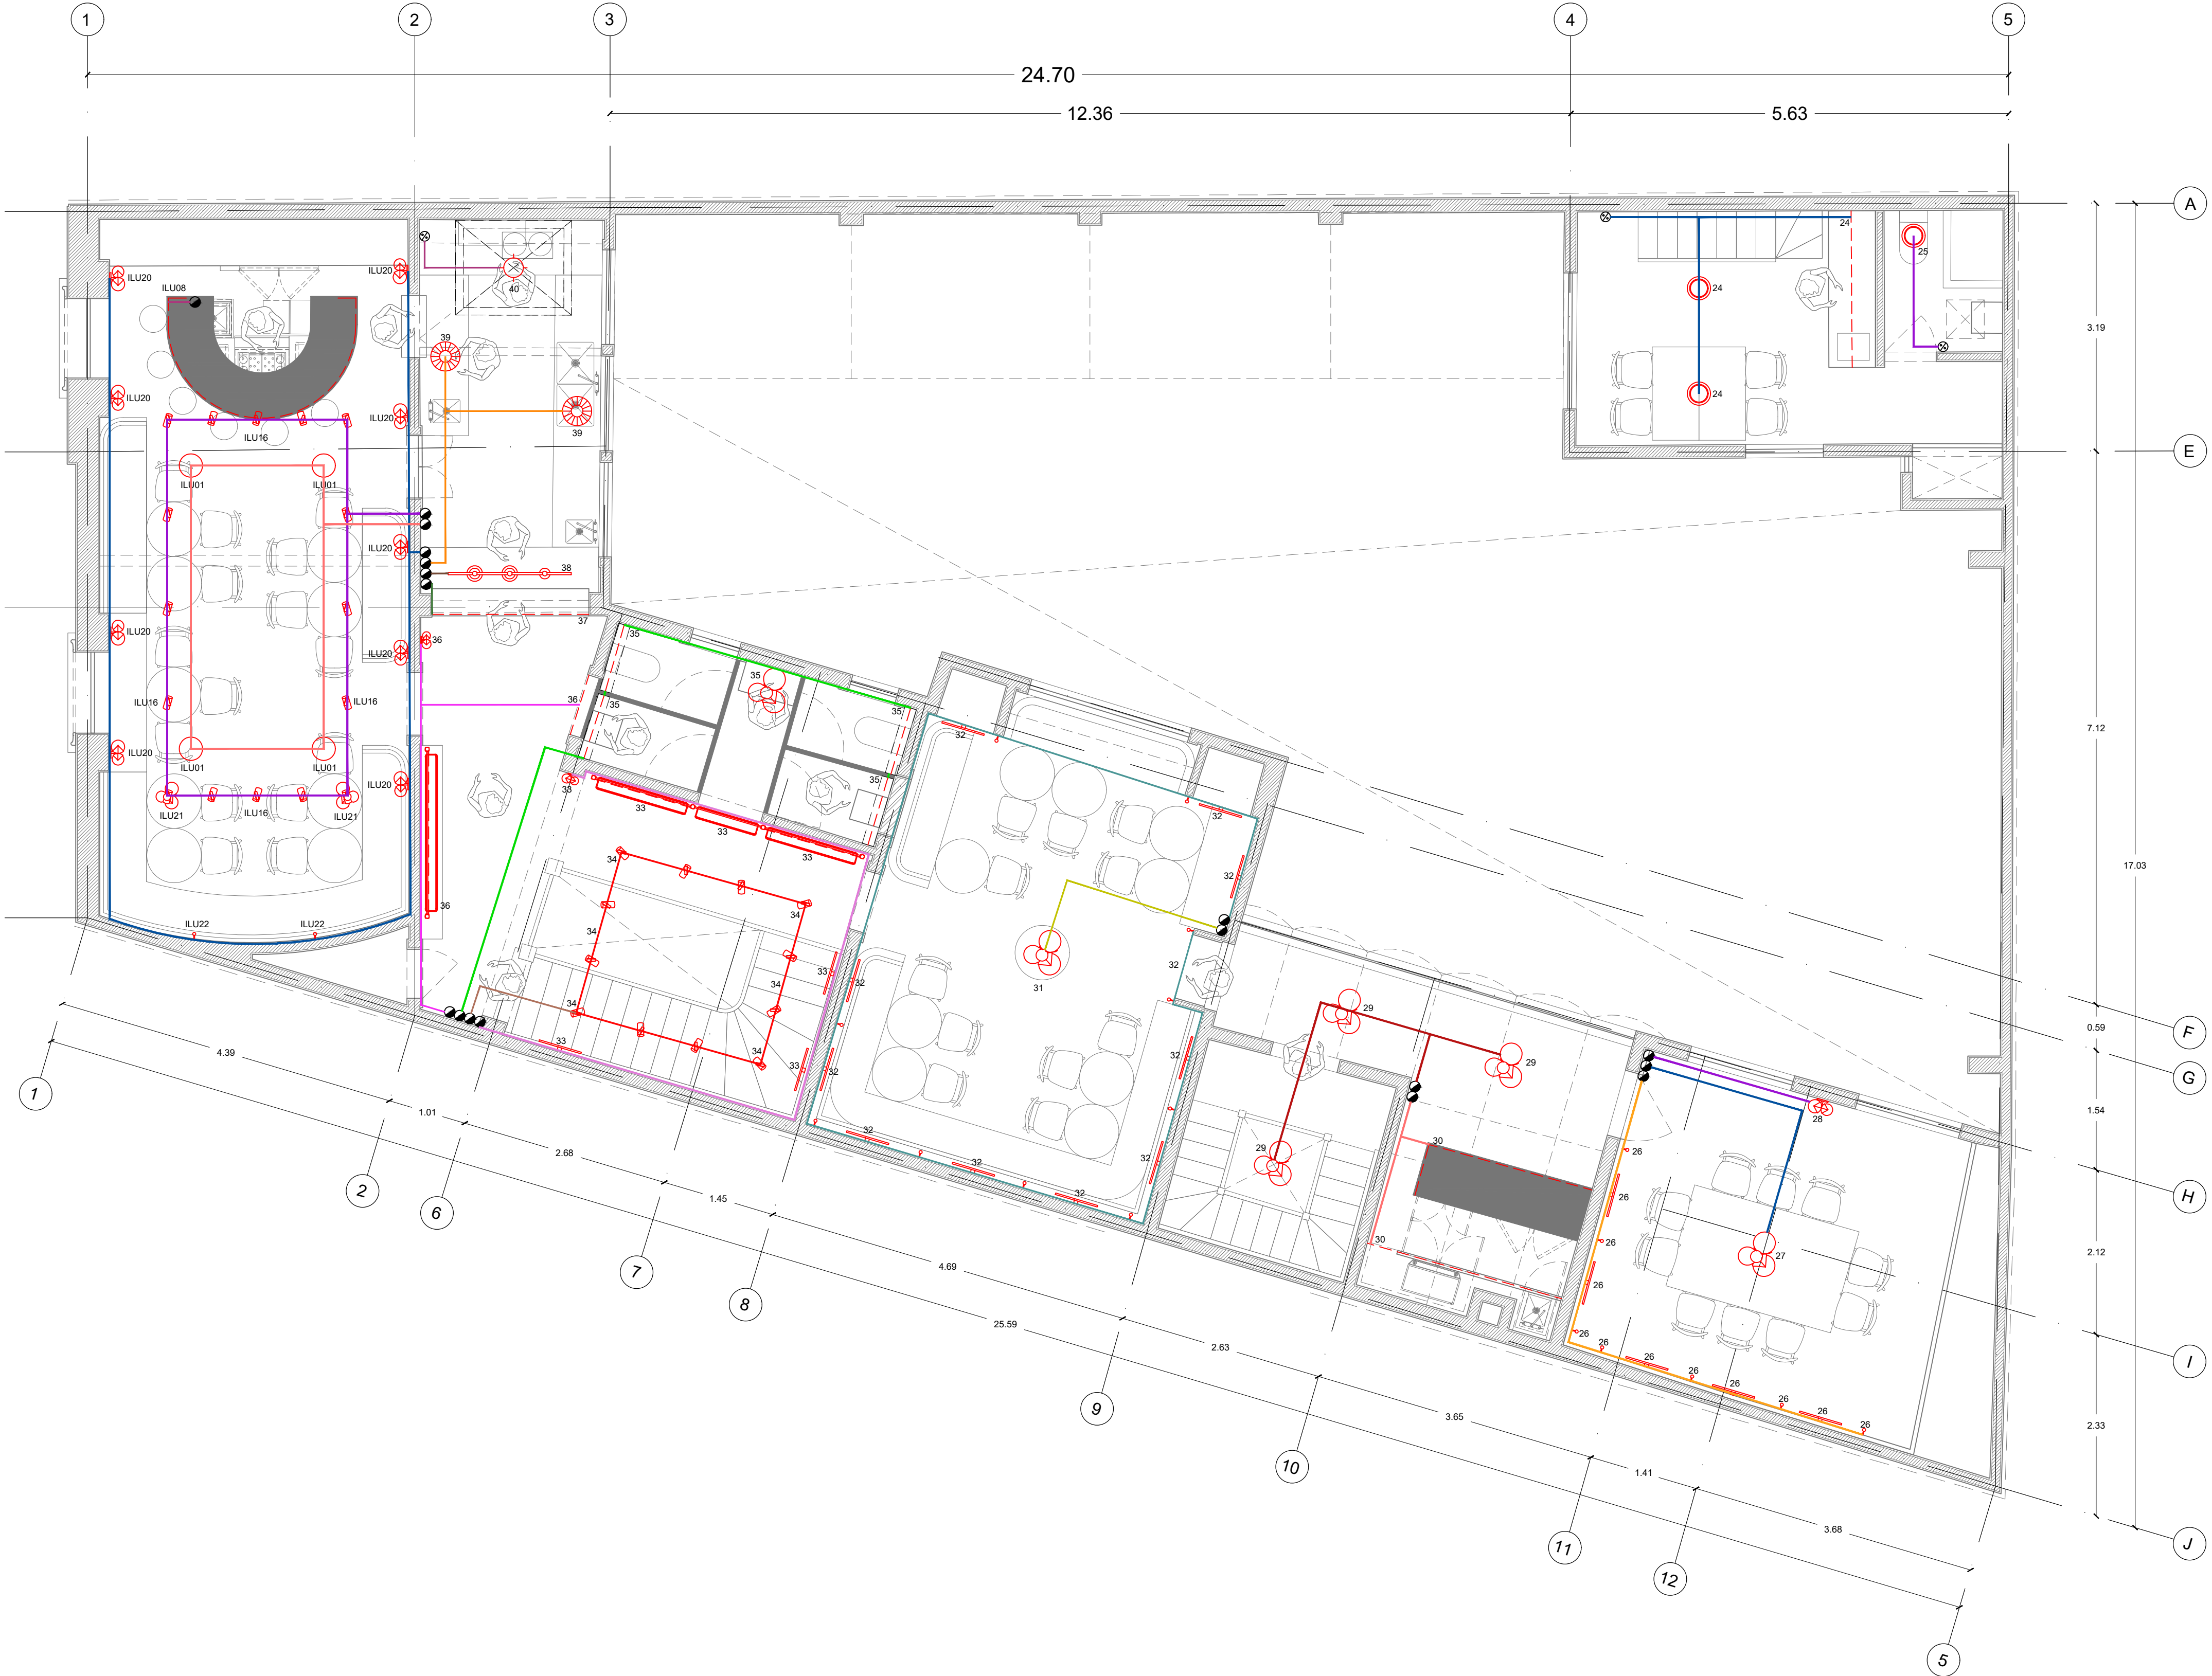

PLANTA PRIMER NIVEL DE CONTROL DE ILUMINACIÓN
PASTICCIO
ESCALA 1:75

NORTE

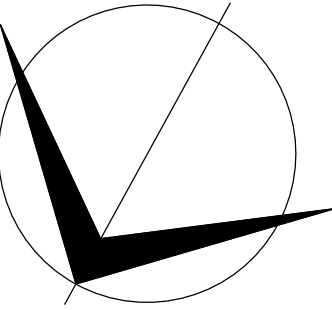

PROYECTO:

PASTICCIO

DOMICILIO:


Praga 33, colonia Juárez Ciudad de México, CDMX

NOTAS GENERALES:

- 1.- LAS COTAS RIGEN AL DIBUJO.
- 2.- LOS PLANOS ARQUITECTÓNICOS RIGEN SOBRE LOS PLANOS DE INGENIERÍAS Y/O ESTRUCTURALES. CUALQUIER DISCREPANCIA DEBERÁ CONSULTARSE CON EL ÁREA DE DISEÑO, Y SUSPENDER EL TRABAJO HASTA QUE LA SOLUCIÓN SEA APROBADA.
- 3.- ANTES DE INICIAR CUALQUIER TRABAJO, DEBERÁN VERIFICARSE EN OBRA LAS MEDIDAS Y NIVELES, SUJETÁNDOSE AL INCISO No. 2.
- 4.- EL CONTRATISTA ES RESPONSABLE DE TRABAJAR SIEMPRE CON UN JUEGO COMPLETO DE PLANOS. CUALQUIER DUDA EN LA INTERPRETACIÓN DE LOS MISMOS, DEBERÁ CONSULTARSE CON LA DIRECCIÓN DE OBRA Y EL ARQUITECTO.
- 5.- TODOS LOS NIVELES ARQUITECTÓNICOS SERÁN REFERIDOS A UN BANCO DE NIVEL DETERMINADO EN OBRA.

SIMBOLOGÍA:

NIVEL DE PISO TERMINADO

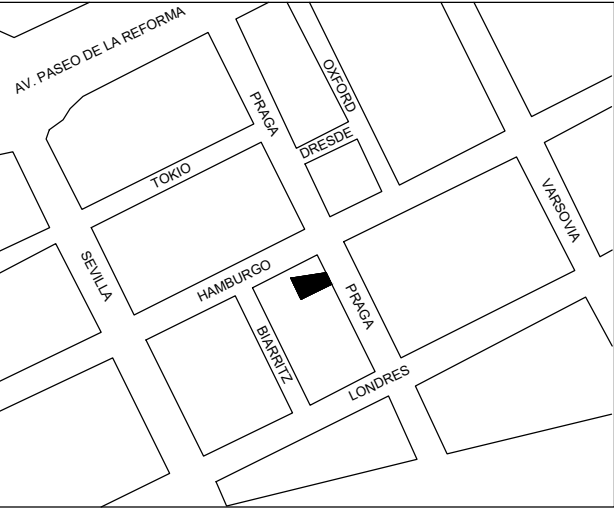

ÁREAS

PROPIETARIO:

DISEÑO:

MYTOLVOK

Plano V. Sec. Miguel Hidalgo CP 11060

TÍTULO:

PLANTA PRIMER NIVEL DE CONTROL DE ILUMINACIÓN

DIBUJO: IAP

REVISÓ:

FECHA: Octubre 27, 2023


ACOTACIÓN: METROS

ESCALA: 1:75


CLAVE:

ILU.05

LISTADO DE CONTROLES						
CONTROL	APAGADO POR	AREA	ACCESORIO	#	W	TOTAL
45	APAGADOR	Lámpara de sobreponer en almacen		6	25 W	150 W
46	APAGADOR	Lámpara de sobreponer en escalera servicio		4	25 W	100 W
47	DIMMER	Lámpara de cánope en muro en fachada		5	10 W	50 W
48	APAGADOR	Lámpara de sobreponer en site		1	25 W	25 W
49	APAGADOR	Lámpara de sobreponer en oficina		2	25 W	50 W
50	APAGADOR	Lámpara de sobreponer en wc lockers		2	25 W	50 W
51	APAGADOR	Lámpara de sobreponer en lockers		2	25 W	50 W
52	APAGADOR	Lámpara de sobreponer en wc lockers		2	25 W	50 W

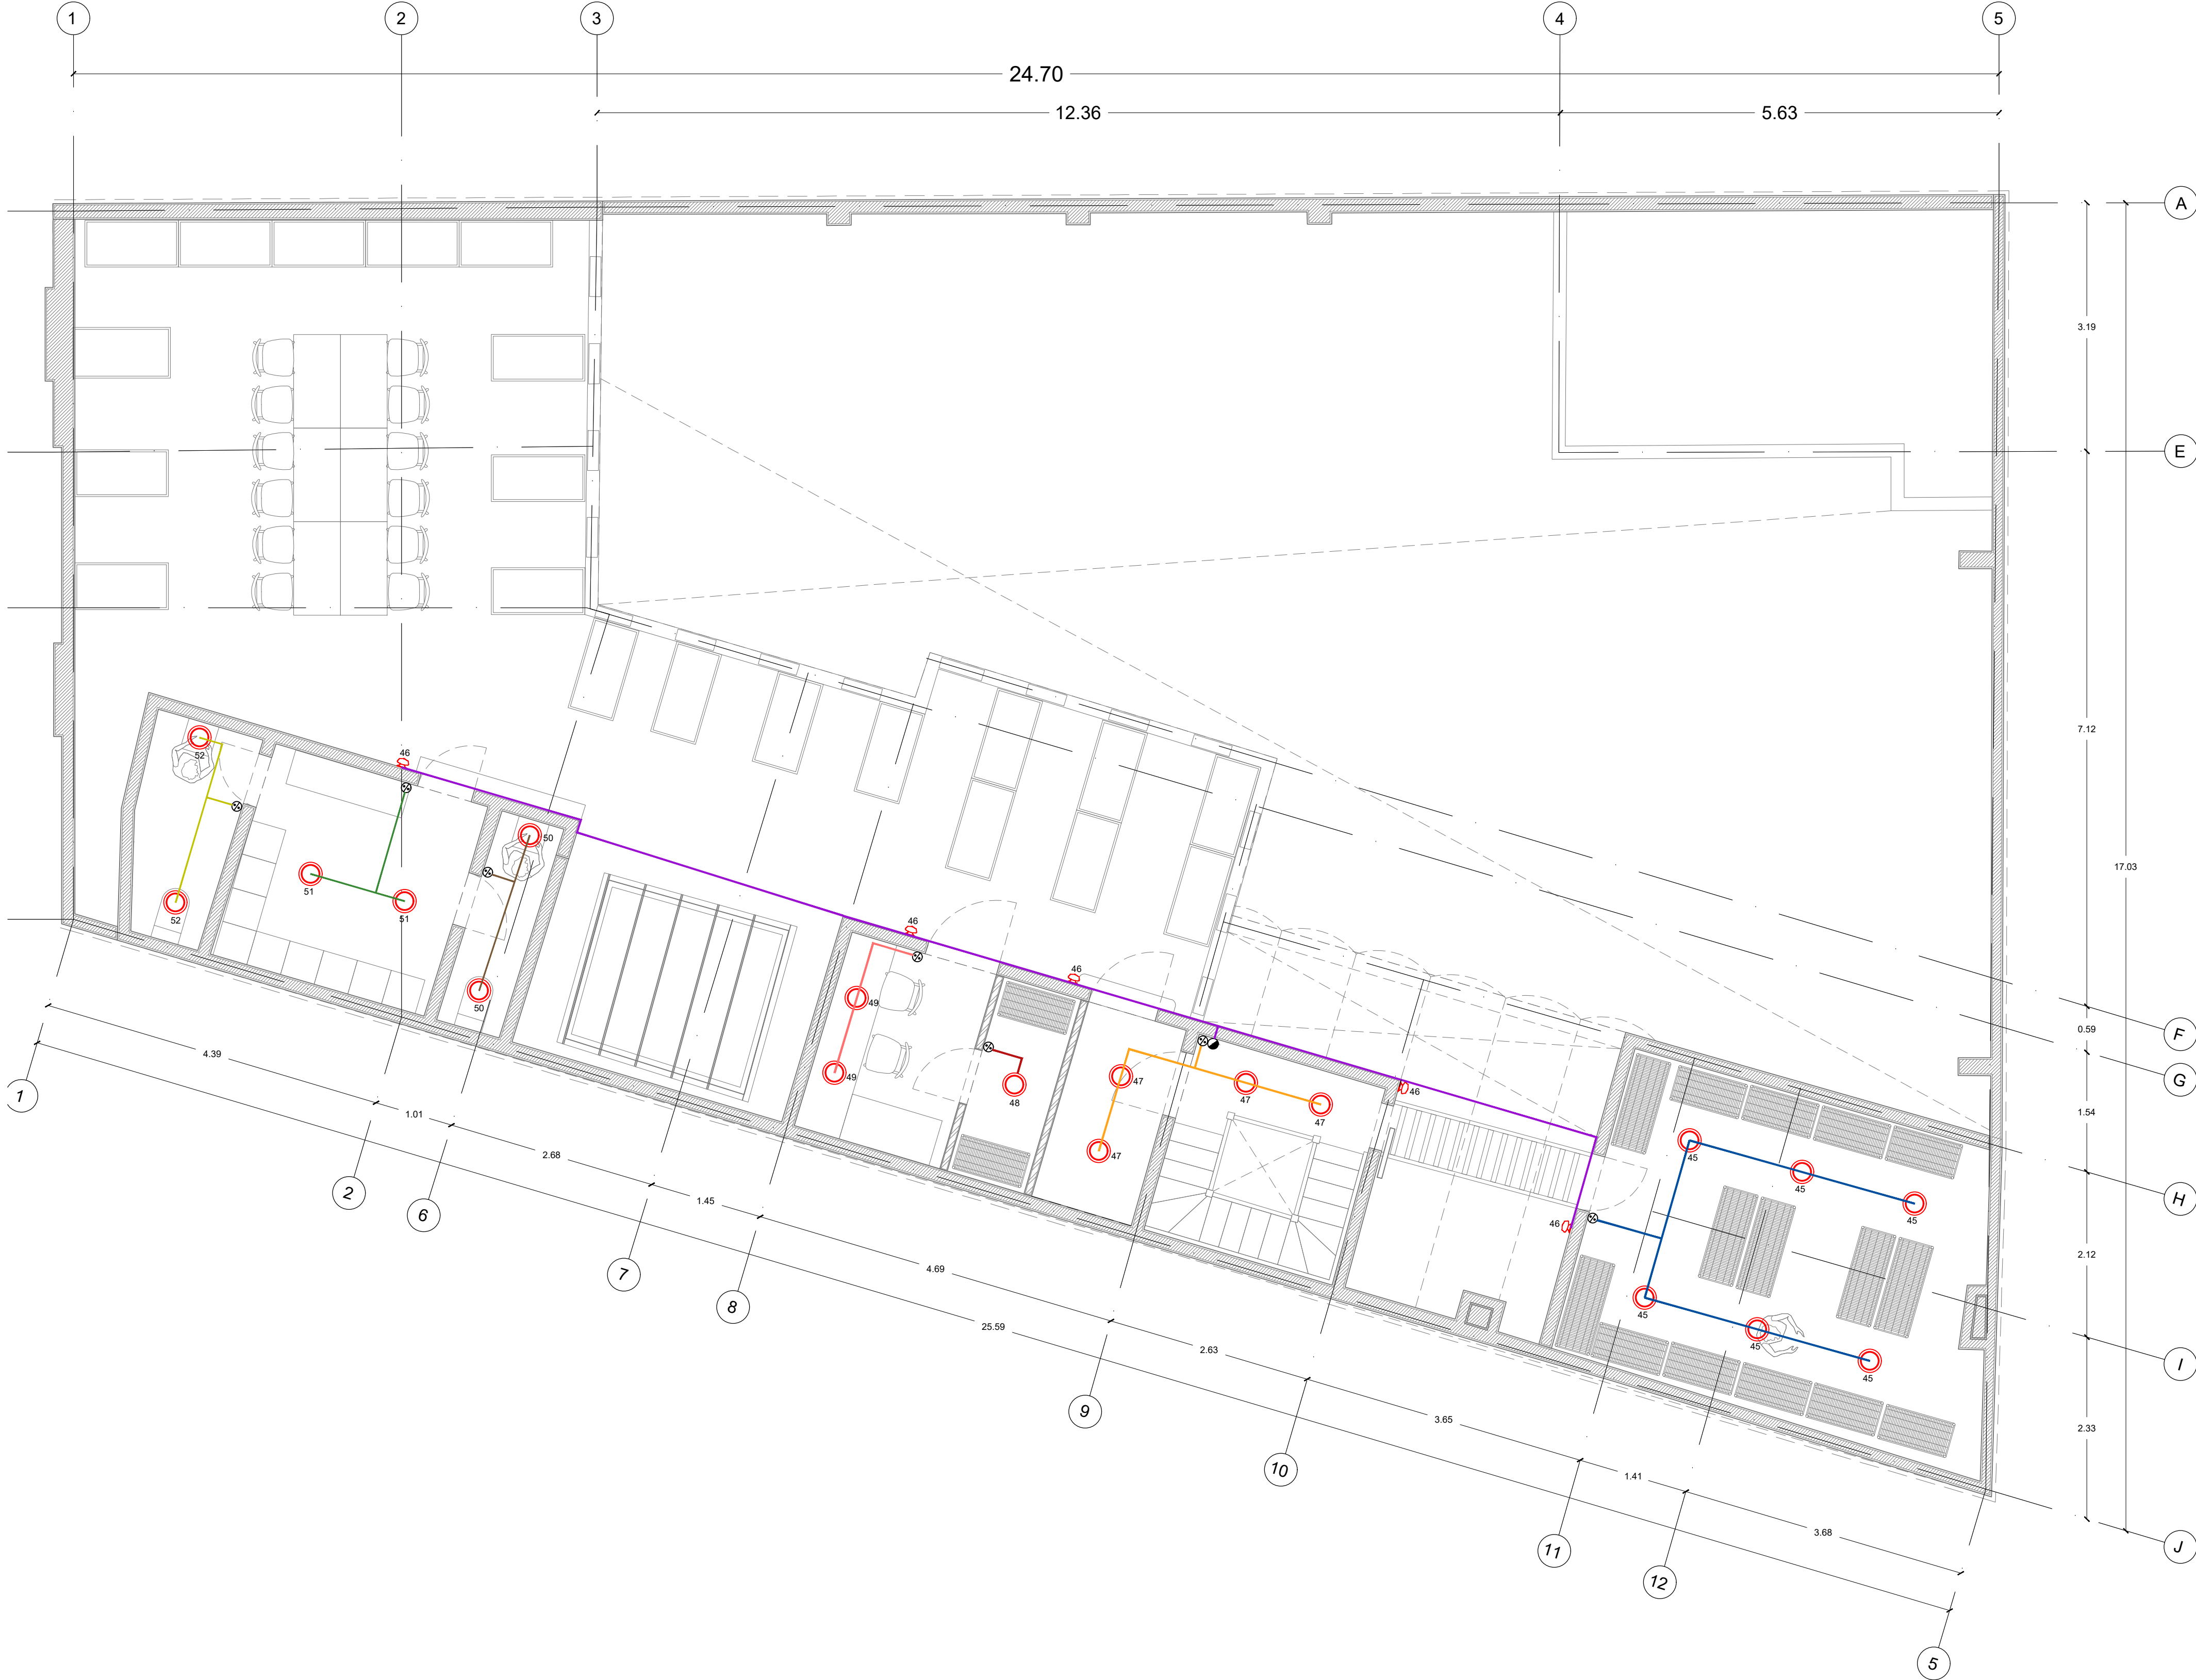

PLANTA SEGUNDO NIVEL DE CONTROL DE ILUMINACIÓN
PASTICCIO
ESCALA 1:75

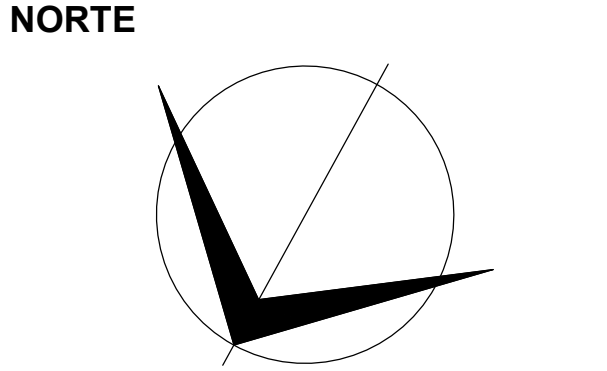

PROYECTO:

PASTICCIO


DOMICILIO:
Praga 33, colonia Juárez Ciudad de México, CDMX

NOTAS GENERALES:

- 1.- LAS COTAS RIGEN AL DIBUJO.
- 2.- LOS PLANOS ARQUITECTÓNICOS RIGEN SOBRE LOS PLANOS DE INGENIERÍAS Y/O ESTRUCTURALES. CUALQUIER DISCREPANCIA DEBERÁ CONSULTARSE CON EL ÁREA DE DISEÑO, Y SUSPENDER EL TRABAJO HASTA QUE LA SOLUCIÓN SEA APROBADA.
- 3.- ANTES DE INICIAR CUALQUIER TRABAJO, DEBERÁN VERIFICARSE EN OBRA LAS MEDIDAS Y NIVELES, SUJETÁNDOSE AL INCISO No. 2.
- 4.- EL CONTRATISTA ES RESPONSABLE DE TRABAJAR SIEMPRE CON UN JUEGO COMPLETO DE PLANOS. CUALQUIER DUDA EN LA INTERPRETACIÓN DE LOS MISMOS, DEBERÁ CONSULTARSE CON LA DIRECCIÓN DE OBRA Y EL ARQUITECTO.
- 5.- TODOS LOS NIVELES ARQUITECTÓNICOS SERÁN REFERIDOS A UN BANCO DE NIVEL DETERMINADO EN OBRA.

SIMBOLOGÍA:

NIVEL DE PISO TERMINADO

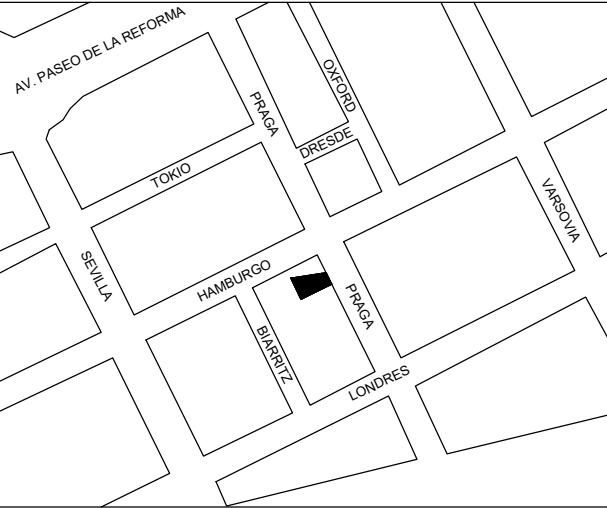

ÁREAS

PROPIETARIO:

DISEÑO:

MYTELVAK

Plano V. Sec. Miguel Hidalgo CP 11960

TÍTULO: PLANTA SEGUNDO NIVEL DE CONTROL DE ILUMINACIÓN

DIBUJÓ: IAP REVISÓ:

FECHA: Octubre 27, 2023

ACOTACIÓN: METROS ESCALA: 1:75
CLAVE:


ILU.06

SIMBOLOGÍA MUROS		
CLAVE	SIMBOLOGÍA	TIPO
A		Panel sándwich para cámara refrigerada, espesor de panel de 4", densidad de panel de 42 kg por CBM
B		Muro nuevo con bastidor estructural formado con poste metálico Perfil Rey 6.35 (2-1/2") calibre 26 espaciados @ 61.00 cm (24") dentro de canales de amarre Perfil Rey 6.35 (2-1/2") calibre 26 superior e inferior, unidos con tornillos marca Tornipanel tipo framer de 1/2". Los canales se fijan a piso y losa/cubierta con anclaje adecuado @ 61.00 cm (24"). El bastidor se forrará por ambos lados con una capa de panel de cemento Durock regular de 12.7mm de espesor; la fijación se hará con Tornillos Tornipanel tipo STD de 1" espaciados @ 30.5 cm (12"). Las juntas entre paneles se tratarán con compuesto para juntas Ready Mix estándar plus Panel Rey y cinta de refuerzo de uniones marca Panel Rey únicamente en la última capa. Las cabezas de los tornillos se cubrirán con compuesto
C		Muro nuevo con bastidor estructural formado con poste metálico Perfil Rey 6.35 (2-1/2") calibre 26 espaciados @ 61.00 cm (24") dentro de canales de amarre Perfil Rey 6.35 (2-1/2") calibre 26 superior e inferior, unidos con tornillos marca Tornipanel tipo framer de 1/2". Los canales se fijan a piso y losa/cubierta con anclaje adecuado @ 61.00 cm (24"). El bastidor se forrará por ambos lados con una capa de panel de yeso Panel Rey regular de 12.7mm de espesor; la fijación se hará con Tornillos Tornipanel tipo STD de 1" espaciados @ 30.5 cm (12"). Las juntas entre paneles se tratarán con compuesto para juntas Ready Mix estándar plus Panel Rey y cinta de refuerzo de uniones marca Panel Rey únicamente en la última capa. Las cabezas de los tornillos se cubrirán con compuesto


MUROS, MURETES Y FALDONES DE TABLAROCA				
CLAVE	DESCRIPCIÓN	LONGITUD	ALTURA	M2
A01	Panel sándwich para cámara refrigerada	1.49	2.00	2.98
A02	Panel sándwich para cámara refrigerada	0.49	2.00	0.98
A03	Panel sándwich para cámara refrigerada	2.88	2.00	5.76
A04	Panel sándwich para cámara refrigerada	2.25	2.00	4.50
A05	Panel sándwich para cámara refrigerada	0.70	2.00	1.40
A06	Panel sándwich para cámara refrigerada	0.70	2.00	1.40
A07	Panel sándwich para cámara refrigerada	2.25	2.00	4.50
A08	Panel sándwich para cámara refrigerada	2.08	4.09	8.51
A09	Panel sándwich para cámara refrigerada	2.08	4.09	8.51
A10	Panel sándwich para cámara refrigerada	1.62	4.09	6.63
A11	Panel sándwich para cámara refrigerada	0.58	4.09	2.37
A12	Panel sándwich para cámara refrigerada	0.30	4.09	1.23
B01	Muro de durock a dos caras	3.41	3.40	11.59
B02	Muro de durock a dos caras	0.89	4.09	3.64
B03	Murete de durock a dos caras	1.95	1.00	1.95
B04	Murete de durock a dos caras	4.38	1.00	4.38
B05	Murete de durock a dos caras	0.80	1.00	0.80
B06	Muro de durock a dos caras	3.01	2.00	6.02
B07	Murete de durock a dos caras	1.50	1.00	1.50
B08	Murete de durock a dos caras	3.20	1.00	3.20
B09	Murete de durock a dos caras	0.90	1.00	0.90
				82.74

PLANTA BAJA DE MUROS, MURETES, LAMBRINES Y FALDONES DE TABLAROCA
PASTICCIO

ESCALA 1:75

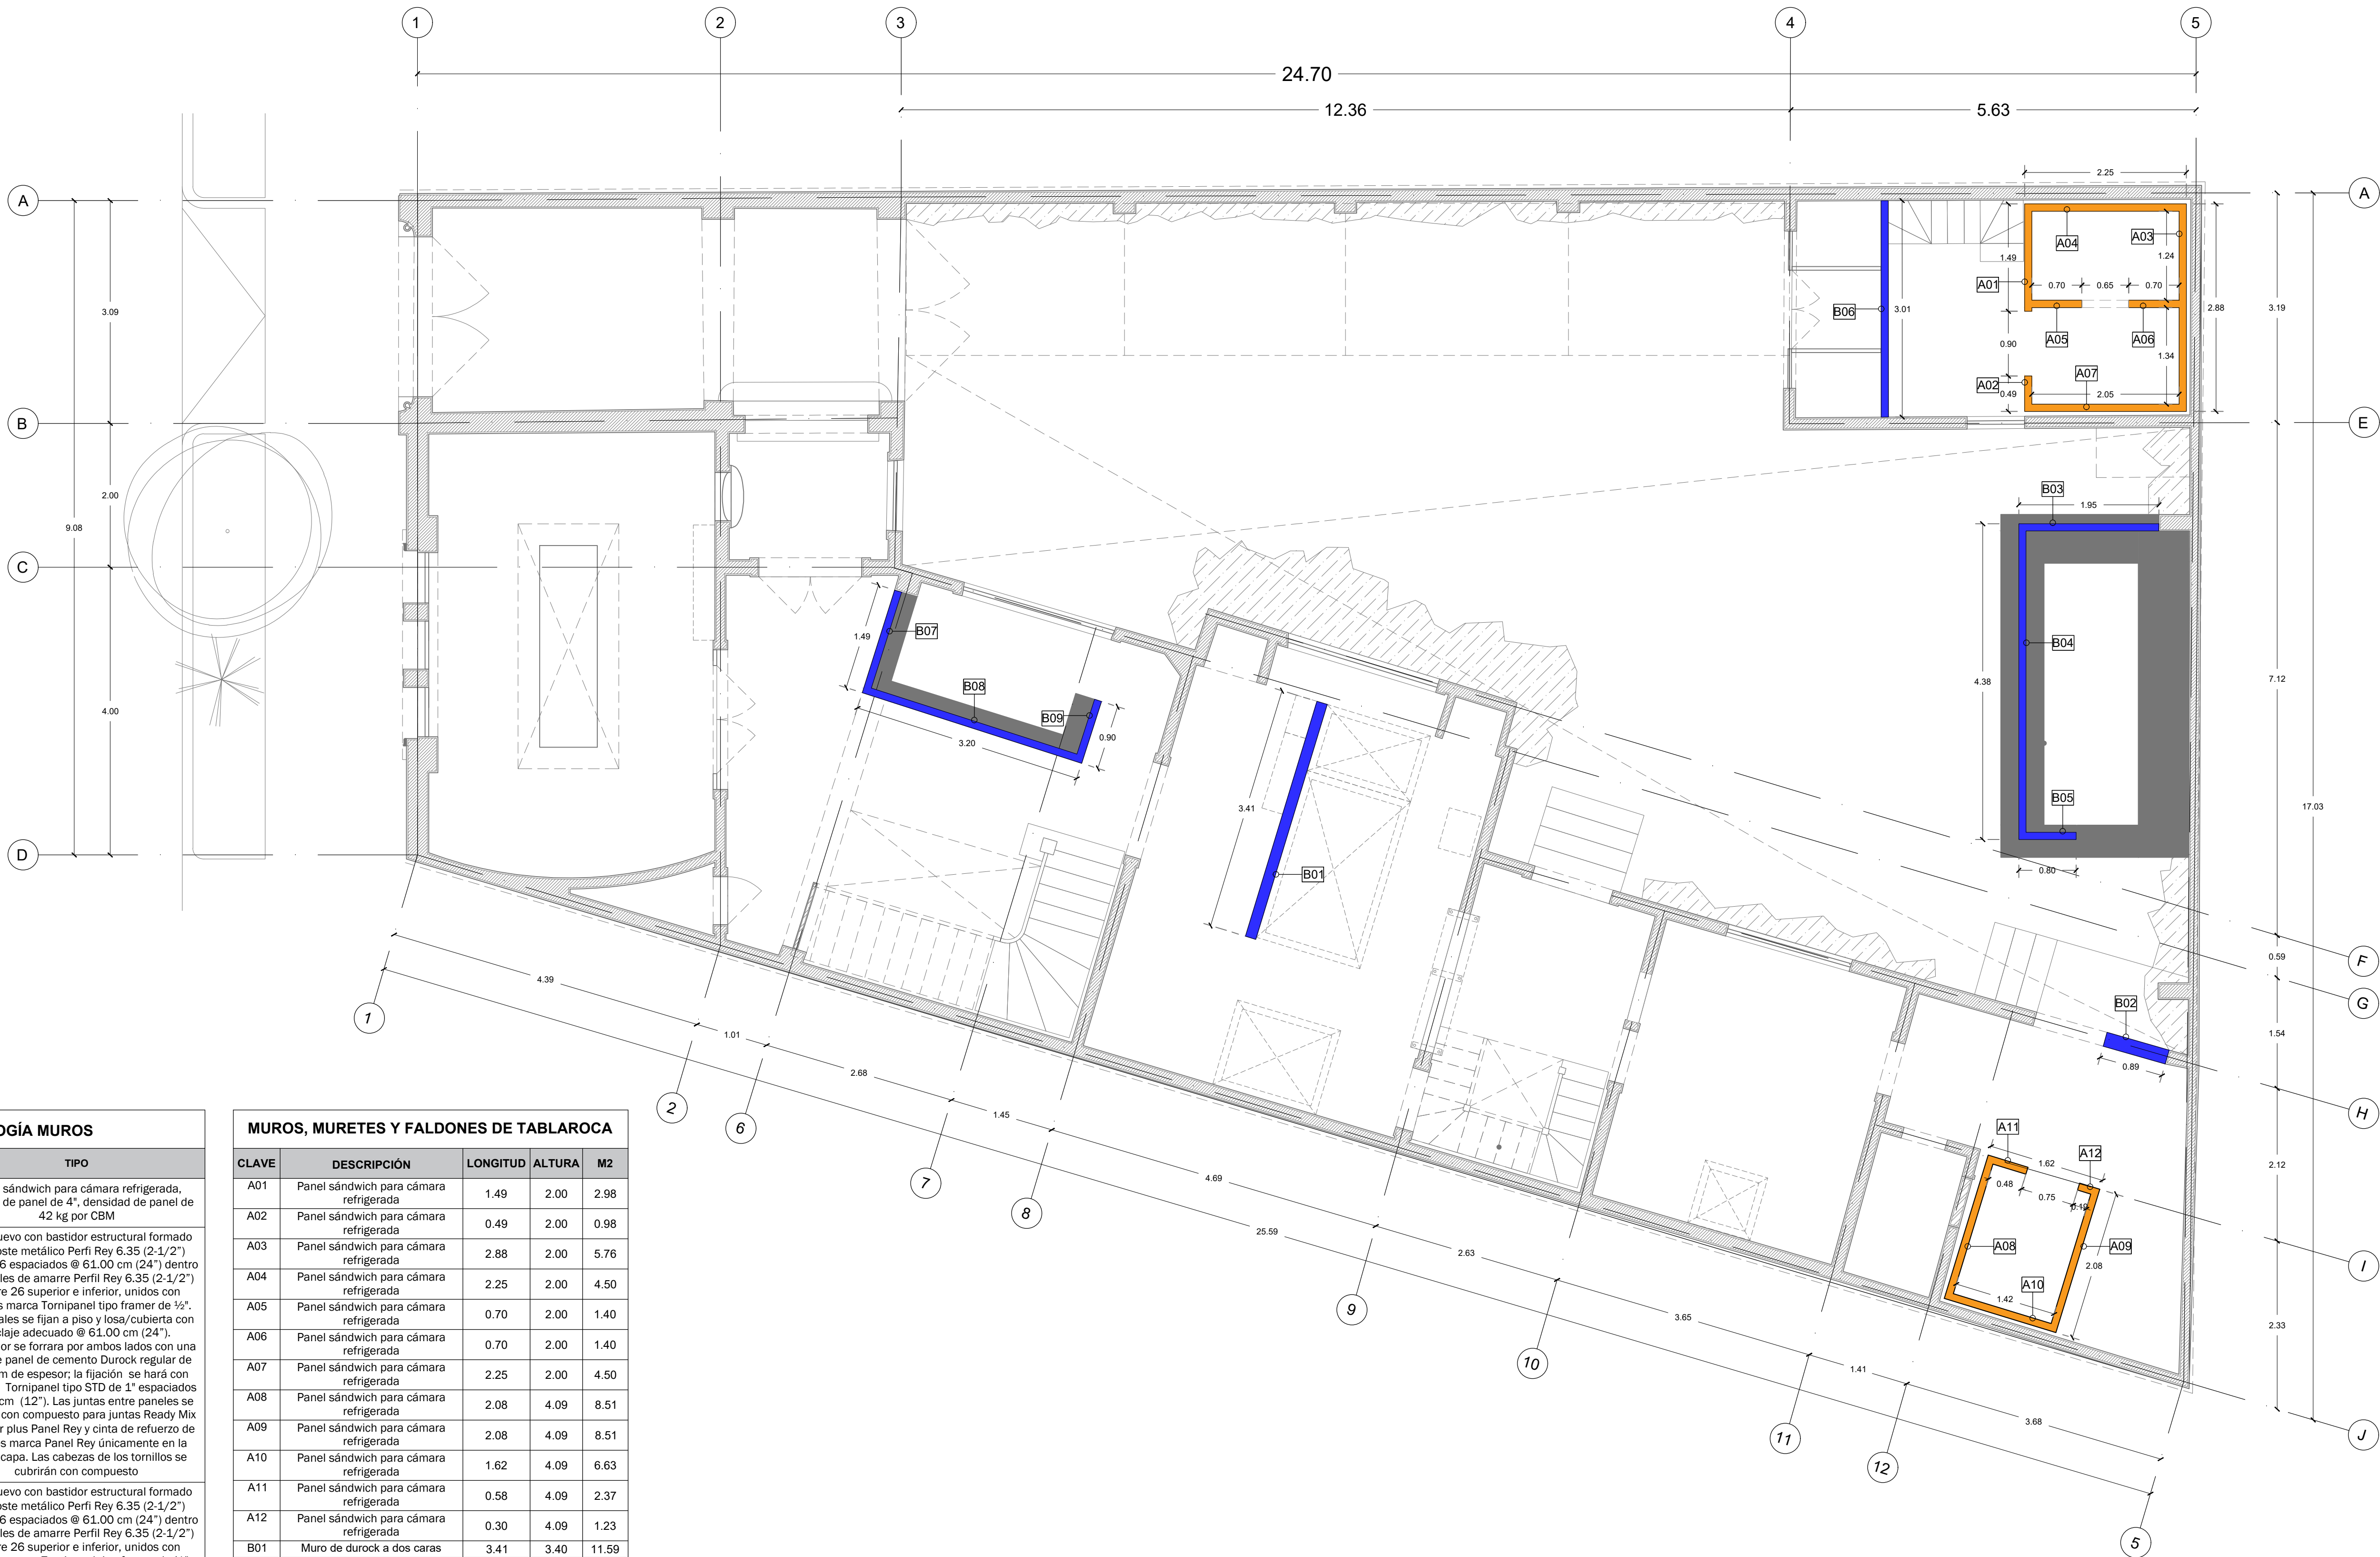

NORTE

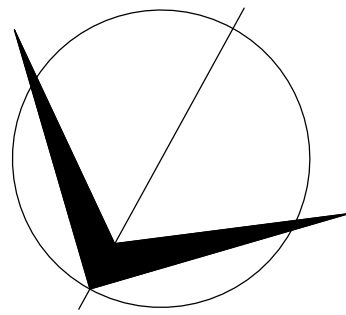

PROYECTO:

PASTICCIO

DOMICILIO:


Praga 33, colonia Juárez Ciudad de México, CDMX

NOTAS GENERALES:

- 1.- LAS COTAS RIGEN AL DIBUJO.
- 2.- LOS PLANOS ARQUITECTÓNICOS RIGEN SOBRE LOS PLANOS DE INGENIERÍAS Y/O ESTRUCTURALES. CUALQUIER DISCREPANCIA DEBERÁ CONSULTARSE CON EL ÁREA DE DISEÑO, Y SUSPENDER EL TRABAJO HASTA QUE LA SOLUCIÓN SEA APROBADA.
- 3.- ANTES DE INICIAR CUALQUIER TRABAJO, DEBERÁN VERIFICARSE EN OBRA LAS MEDIDAS Y NIVELES, SUJETÁNDOSE AL INCISO No. 2.
- 4.- EL CONTRATISTA ES RESPONSABLE DE TRABAJAR SIEMPRE CON UN JUEGO COMPLETO DE PLANOS. CUALQUIER DUDA EN LA INTERPRETACIÓN DE LOS MISMOS, DEBERÁ CONSULTARSE CON LA DIRECCIÓN DE OBRA Y EL ARQUITECTO.
- 5.- TODOS LOS NIVELES ARQUITECTÓNICOS SERÁN REFERIDOS A UN BANCO DE NIVEL DETERMINADO EN OBRA.

SIMBOLOGÍA:

NIVEL DE PISO TERMINADO

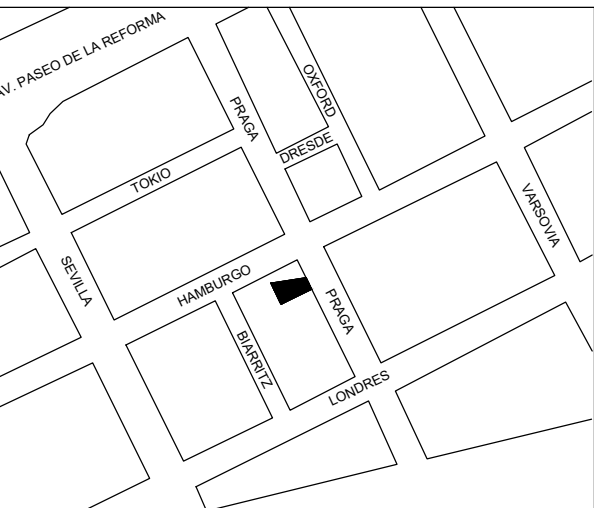

ÁREAS

PROPIETARIO:

DISEÑO:

MYTELVDK

Plano V Sec. Miguel Hidalgo CP-11560

TÍTULO:

PLANTA BAJA DE MUROS, MURETES, LAMBRINES Y FALDONES DE TABLAROCA

DIBUJO: IAP

REVISÓ:

FECHA: Noviembre 03, 2023

ACOTACIÓN: METROS

ESCALA: 1:75

CLAVE:

TBR.01


SIMBOLOGÍA MUROS		
CLAVE	SIMBOLOGÍA	TIPO
A		Panel sándwich para cámara refrigerada, espesor de panel de 4", densidad de panel de 42 kg por CBM
B		Muro nuevo con bastidor estructural formado con poste metálico Perfil Rey 6.35 (2-1/2") calibre 26 espaciados @ 61.00 cm (24") dentro de canales de amarre Perfil Rey 6.35 (2-1/2") calibre 26 superior e inferior, unidos con tornillos marca Tornipanel tipo framer de 1/2". Los canales se fijan a piso y losa/cubierta con anclaje adecuado @ 61.00 cm (24"). El bastidor se forrará por ambos lados con una capa de panel de cemento Durock regular de 12.7mm de espesor; la fijación se hará con Tornillos Tornipanel tipo STD de 1" espaciados @ 30.5 cm (12"). Las juntas entre paneles se tratarán con compuesto para juntas Ready Mix estándar plus Panel Rey y cinta de refuerzo de uniones marca Panel Rey únicamente en la última capa. Las cabezas de los tornillos se cubrirán con compuesto
C		Muro nuevo con bastidor estructural formado con poste metálico Perfil Rey 6.35 (2-1/2") calibre 26 espaciados @ 61.00 cm (24") dentro de canales de amarre Perfil Rey 6.35 (2-1/2") calibre 26 superior e inferior, unidos con tornillos marca Tornipanel tipo framer de 1/2". Los canales se fijan a piso y losa/cubierta con anclaje adecuado @ 61.00 cm (24"). El bastidor se forrará por ambos lados con una capa de panel de yeso Panel Rey regular de 12.7mm de espesor; la fijación se hará con Tornillos Tornipanel tipo STD de 1" espaciados @ 30.5 cm (12"). Las juntas entre paneles se tratarán con compuesto para juntas Ready Mix estándar plus Panel Rey y cinta de refuerzo de uniones marca Panel Rey únicamente en la última capa. Las cabezas de los tornillos se cubrirán con compuesto

MUROS, MURETES Y FALDONES DE TABLAROCA				
CLAVE	DESCRIPCIÓN	LONGITUD	ALTURA	M2
B10	Murete de durock a dos caras	3.82	1.00	3.82
B11	Muro de durock a dos caras	0.78	3.20	2.50
B12	Murete de durock a dos caras	0.70	1.00	0.70
B13	Murete de durock a dos caras	2.19	1.00	2.19
				9.21

PLANTA ALTA DE MUROS, MURETES, LAMBRINES Y FALDONES DE TABLAROCA
PASTICCIO

ESCALA 1:75

NORTE

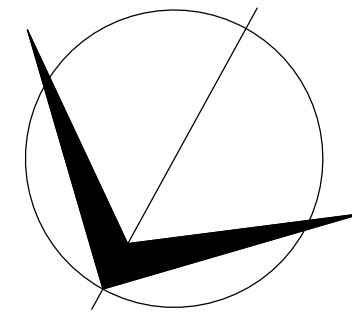

PROYECTO:

PASTICCIO

DOMICILIO:


Praga 33, colonia Juárez Ciudad de México, CDMX

NOTAS GENERALES:

- 1.- LAS COTAS RIGEN AL DIBUJO.
- 2.- LOS PLANOS ARQUITECTÓNICOS RIGEN SOBRE LOS PLANOS DE INGENIERÍAS Y/O ESTRUCTURALES. CUALQUIER DISCREPANCIA DEBERÁ CONSULTARSE CON EL ÁREA DE DISEÑO, Y SUSPENDER EL TRABAJO HASTA QUE LA SOLUCIÓN SEA APROBADA.
- 3.- ANTES DE INICIAR CUALQUIER TRABAJO, DEBERÁN VERIFICARSE EN OBRA LAS MEDIDAS Y NIVELES, SUJETÁNDOSE AL INCISO No. 2.
- 4.- EL CONTRATISTA ES RESPONSABLE DE TRABAJAR SIEMPRE CON UN JUEGO COMPLETO DE PLANOS. CUALQUIER DUDA EN LA INTERPRETACIÓN DE LOS MISMOS, DEBERÁ CONSULTARSE CON LA DIRECCIÓN DE OBRA Y EL ARQUITECTO.
- 5.- TODOS LOS NIVELES ARQUITECTÓNICOS SERÁN REFERIDOS A UN BANCO DE NIVEL DETERMINADO EN OBRA.

SIMBOLOGÍA:

NIVEL DE PISO TERMINADO

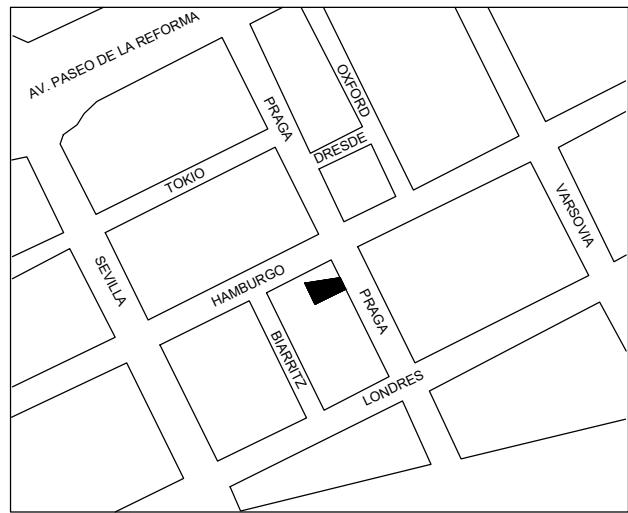

ÁREAS

PROPIETARIO:

DISEÑO:

MYTELVAK

Plano y Sec. Miguel Hidalgo CP 11560

TÍTULO:

PLANTA ALTA DE MUROS, MURETES, LAMBRINES Y FALDONES DE TABLAROCA

DIBUJO: IAP

REVISÓ:

FECHA: Noviembre 03, 2023

ACOTACIÓN: METROS

ESCALA: 1:75

CLAVE:

TBR.02


SIMBOLOGÍA MUROS		
CLAVE	SIMBOLOGÍA	TIPO
A		Panel sándwich para cámara refrigerada, espesor de panel de 4", densidad de panel de 42 kg por CBM
B		Muro nuevo con bastidor estructural formado con poste metálico Perfil Rey 6.35 (2-1/2") calibre 26 espaciados @ 61.00 cm (24") dentro de canales de amarre Perfil Rey 6.35 (2-1/2") calibre 26 superior e inferior, unidos con tornillos marca Tornipanel tipo framer de 1/2". Los canales se fijan a piso y losa/cubierta con anclaje adecuado @ 61.00 cm (24"). El bastidor se forrará por ambos lados con una capa de panel de cemento Durock regular de 12.7mm de espesor; la fijación se hará con Tornillos Tornipanel tipo STD de 1" espaciados @ 30.5 cm (12"). Las juntas entre paneles se tratarán con compuesto para juntas Ready Mix estándar plus Panel Rey y cinta de refuerzo de uniones marca Panel Rey únicamente en la última capa. Las cabezas de los tornillos se cubrirán con compuesto
C		Muro nuevo con bastidor estructural formado con poste metálico Perfil Rey 6.35 (2-1/2") calibre 26 espaciados @ 61.00 cm (24") dentro de canales de amarre Perfil Rey 6.35 (2-1/2") calibre 26 superior e inferior, unidos con tornillos marca Tornipanel tipo framer de 1/2". Los canales se fijan a piso y losa/cubierta con anclaje adecuado @ 61.00 cm (24"). El bastidor se forrará por ambos lados con una capa de panel de yeso Panel Rey regular de 12.7mm de espesor; la fijación se hará con Tornillos Tornipanel tipo STD de 1" espaciados @ 30.5 cm (12"). Las juntas entre paneles se tratarán con compuesto para juntas Ready Mix estándar plus Panel Rey y cinta de refuerzo de uniones marca Panel Rey únicamente en la última capa. Las cabezas de los tornillos se cubrirán con compuesto

MUROS, MURETES Y FALDONES DE TABLAROCA				
CLAVE	DESCRIPCIÓN	LONGITUD	ALTURA	M2
C01	Muro de tablaroca a dos caras	1.00	2.50	2.50
C02	Muro de tablaroca a dos caras	0.90	2.50	2.25
C03	Muro de tablaroca a dos caras	2.60	2.50	6.50
				11.25

PLANTA DE SEGUNDO NIVEL DE MUROS, MURETES, LAMBRINES Y FALDONES DE TABLAROCA
PASTICCIO

ESCALA 1:75

NORTE

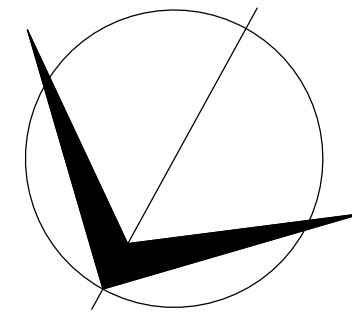

PROYECTO:

PASTICCIO

DOMICILIO:


Praga 33, colonia Juárez Ciudad de México, CDMX

NOTAS GENERALES:

- 1.- LAS COTAS RIGEN AL DIBUJO.
- 2.- LOS PLANOS ARQUITECTÓNICOS RIGEN SOBRE LOS PLANOS DE INGENIERÍAS Y/O ESTRUCTURALES. CUALQUIER DISCREPANCIA DEBERÁ CONSULTARSE CON EL ÁREA DE DISEÑO, Y SUSPENDER EL TRABAJO HASTA QUE LA SOLUCIÓN SEA APROBADA.
- 3.- ANTES DE INICIAR CUALQUIER TRABAJO, DEBERÁN VERIFICARSE EN OBRA LAS MEDIDAS Y NIVELES, SUJETÁNDOSE AL INCISO No. 2.
- 4.- EL CONTRATISTA ES RESPONSABLE DE TRABAJAR SIEMPRE CON UN JUEGO COMPLETO DE PLANOS. CUALQUIER DUDA EN LA INTERPRETACIÓN DE LOS MISMOS, DEBERÁ CONSULTARSE CON LA DIRECCIÓN DE OBRA Y EL ARQUITECTO.
- 5.- TODOS LOS NIVELES ARQUITECTÓNICOS SERÁN REFERIDOS A UN BANCO DE NIVEL DETERMINADO EN OBRA.

SIMBOLOGÍA:

NIVEL DE PISO TERMINADO

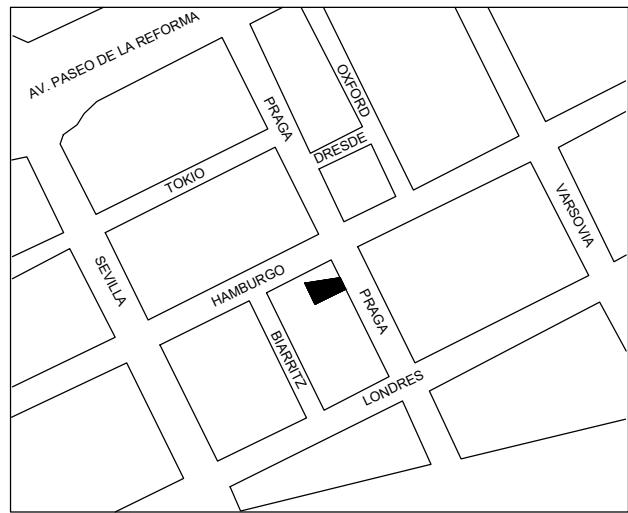

ÁREAS

PROPIETARIO:

DISEÑO:

MYTELVAK

Plano y V. Sec. Miguel Hidalgo CP 11560

TÍTULO:
PLANTA DE SEGUNDO NIVEL
DE MUROS, MURETES,
LAMBRINES Y FALDONES DE
TABLAROCA

DIBUJÓ: IAP

REVISÓ:

FECHA: Noviembre 03, 2023


ACOTACIÓN: METROS

ESCALA: 1:75

CLAVE:

TBR.03

NORTE

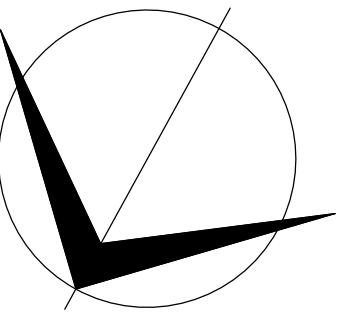

PROYECTO:

PASTICCIO

DOMICILIO:


Praga 33, colonia Juárez Ciudad de México, CDMX

NOTAS GENERALES:

- 1.- LAS COTAS RIGEN AL DIBUJO.
- 2.- LOS PLANOS ARQUITECTÓNICOS RIGEN SOBRE LOS PLANOS DE INGENIERÍAS Y/O ESTRUCTURALES. CUALQUIER DISCREPANCIA DEBERÁ CONSULTARSE CON EL ÁREA DE DISEÑO, Y SUSPENDER EL TRABAJO HASTA QUE LA SOLUCIÓN SEA APROBADA.
- 3.- ANTES DE INICIAR CUALQUIER TRABAJO, DEBERÁN VERIFICARSE EN OBRA LAS MEDIDAS Y NIVELES, SUJETÁNDOSE AL INCISO No. 2.
- 4.- EL CONTRATISTA ES RESPONSABLE DE TRABAJAR SIEMPRE CON UN JUEGO COMPLETO DE PLANOS. CUALQUIER DUDA EN LA INTERPRETACIÓN DE LOS MISMOS, DEBERÁ CONSULTARSE CON LA DIRECCIÓN DE OBRA Y EL ARQUITECTO.
- 5.- TODOS LOS NIVELES ARQUITECTÓNICOS SERÁN REFERIDOS A UN BANCO DE NIVEL DETERMINADO EN OBRA.

SIMBOLOGÍA:

NIVEL DE PISO TERMINADO

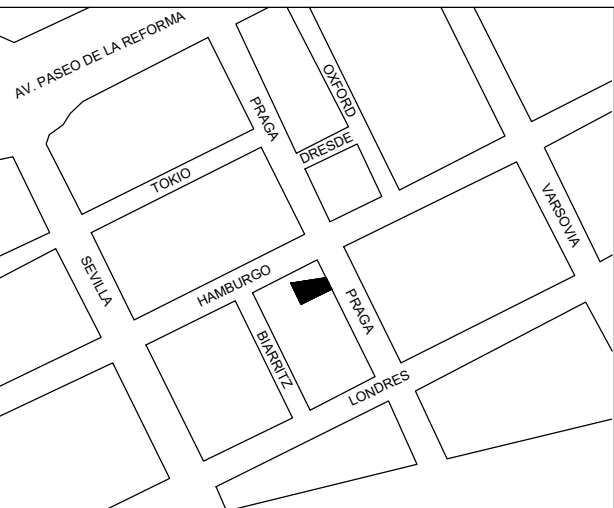

ÁREAS

PROPIETARIO:

DISEÑO:

MYTELVAK

Plano y Sec. Miguel Hidalgo CP 11060

TÍTULO:
PLANTA BAJA DE ACABADOS EN PLAFONES CON DETALLES


DIBUJO: IAP REVISÓ:

FECHA: Noviembre 03, 2023

ACOTACIÓN: METROS ESCALA: 1:75


CLAVE:

PLF.01

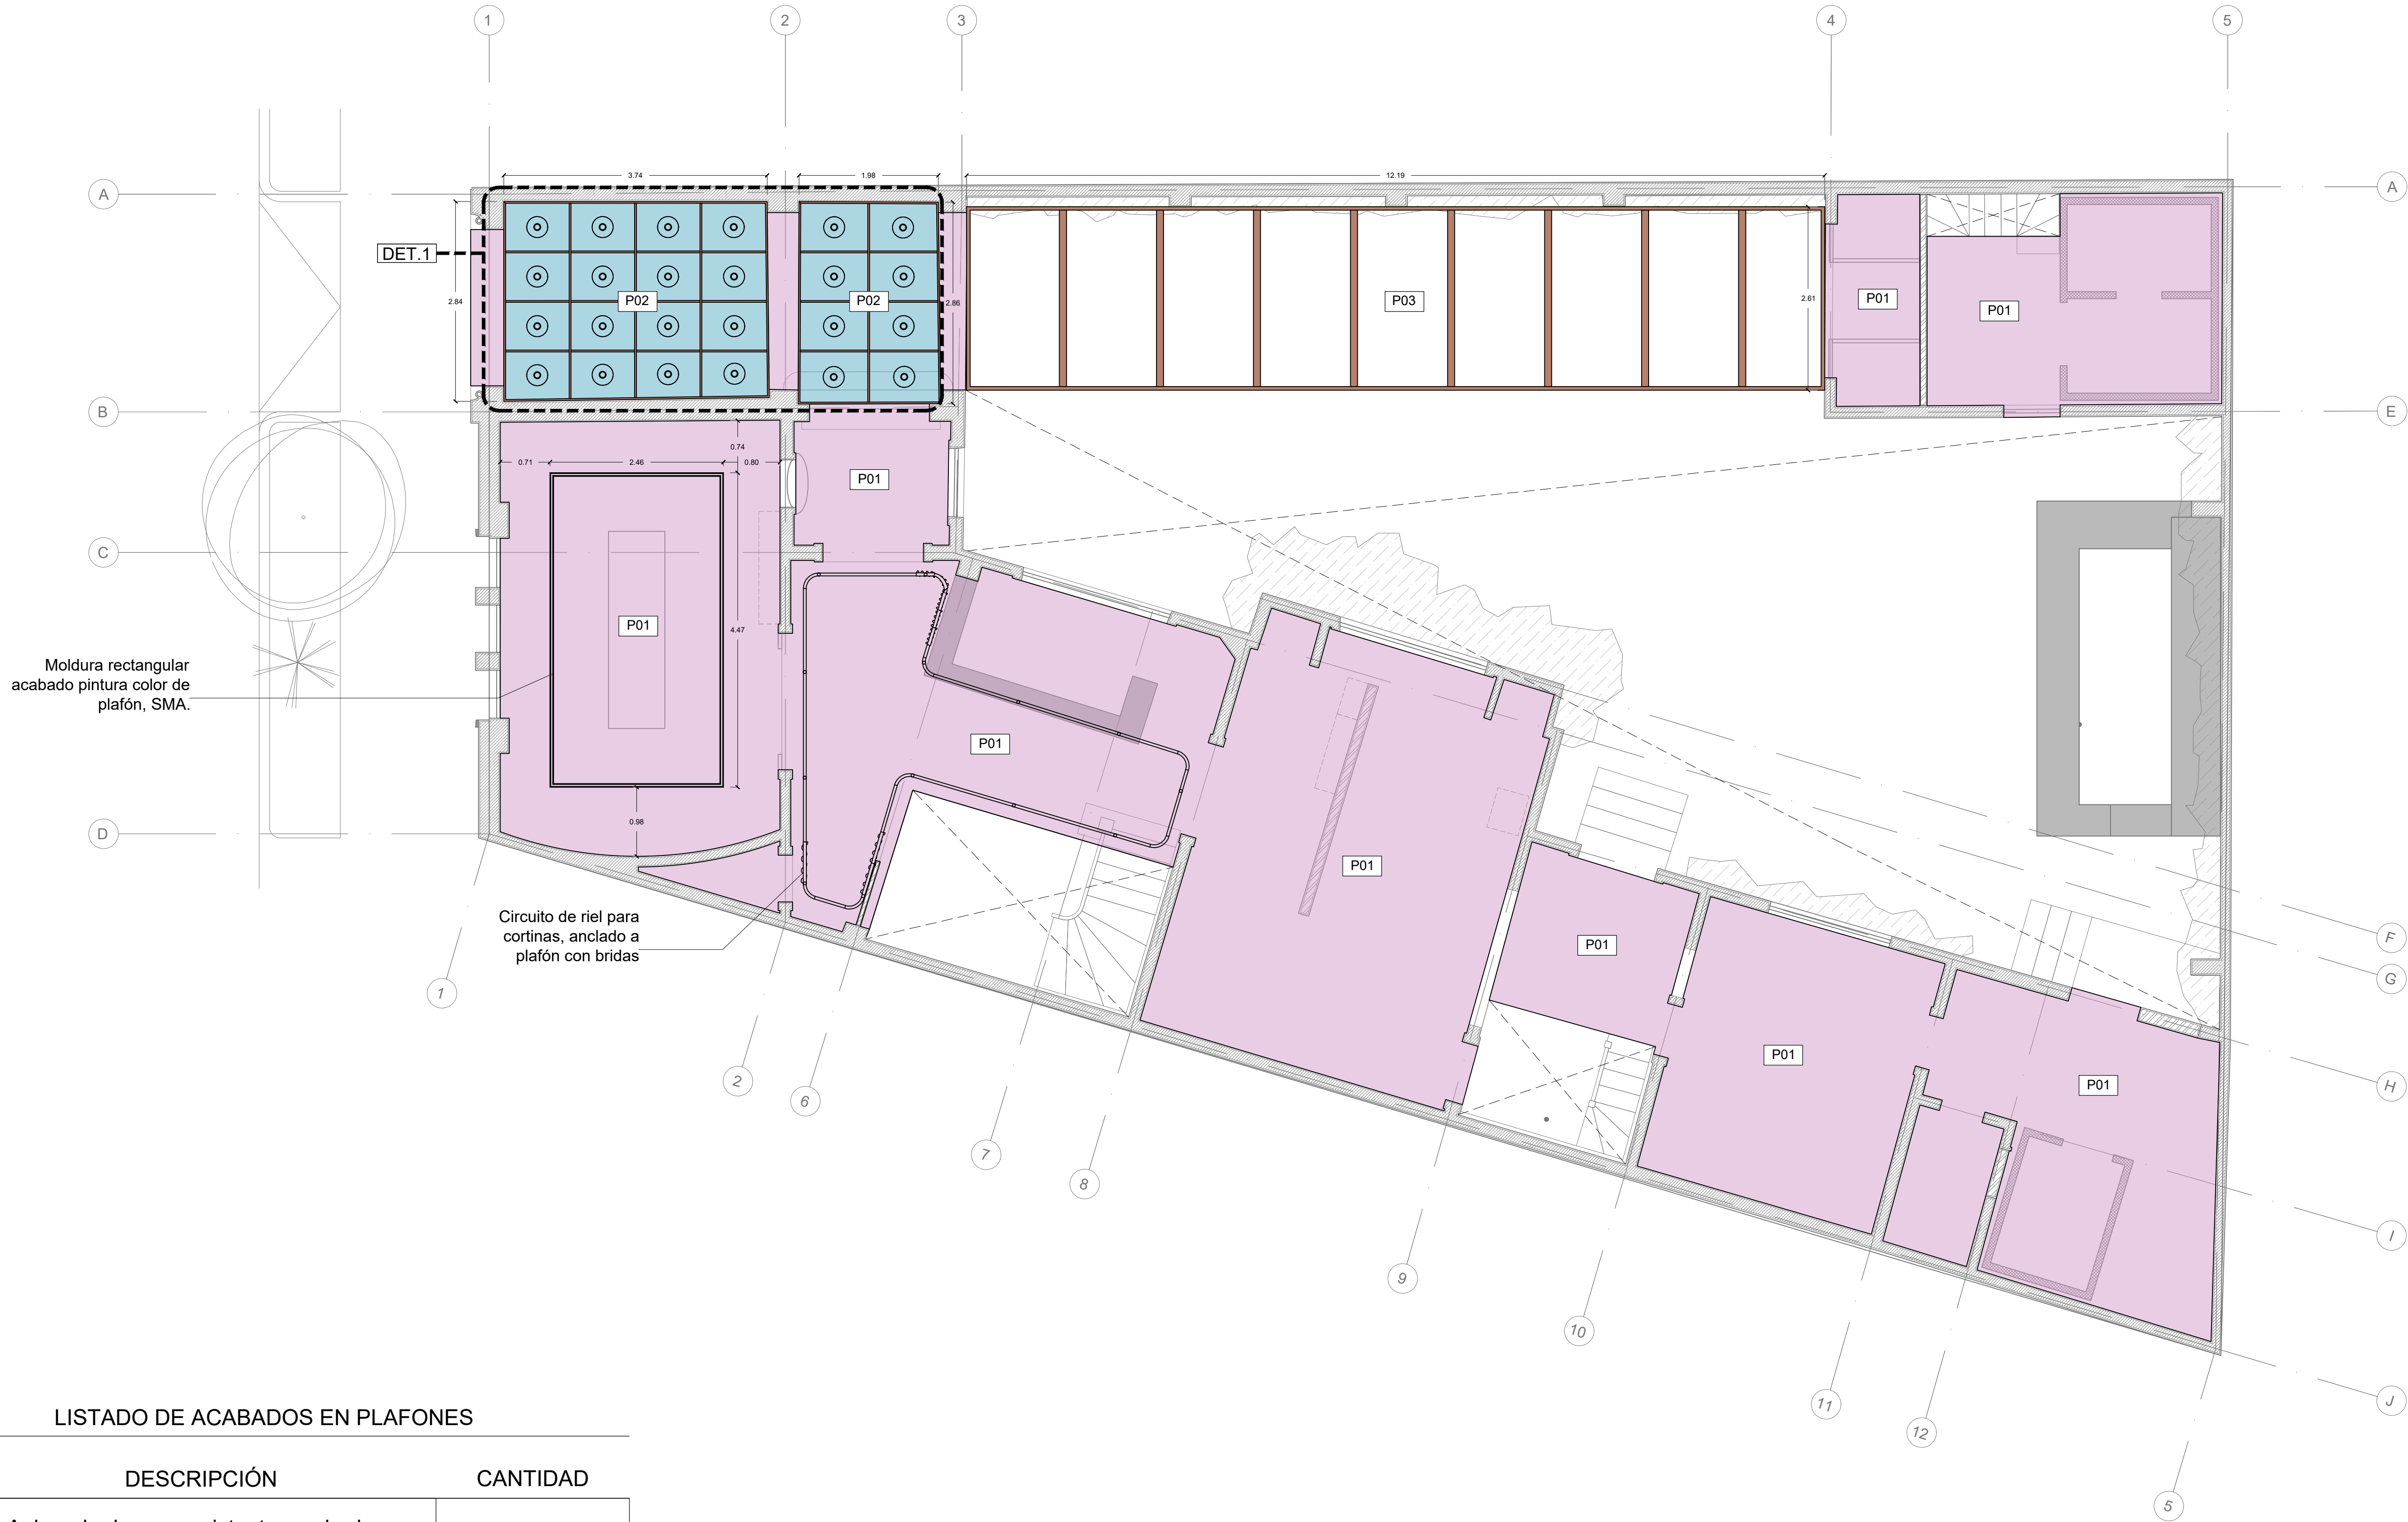

LISTADO DE ACABADOS EN PLAFONES

	DESCRIPCIÓN	CANTIDAD
P01	Aplanado de yeso existente, acabado con pintura vinílica color blanco semi mate, SMA	308.72 m2
P02	Plafón de espejo con retícula de madera maciza, lámparas tipo globo al centro de cada panel	16.31 m2
P03	Estructura para toldo con vegetación	31.76 m2
P04	Plafón de espejo con retícula a base de solera pintada color latón, SMA	26.45 m2

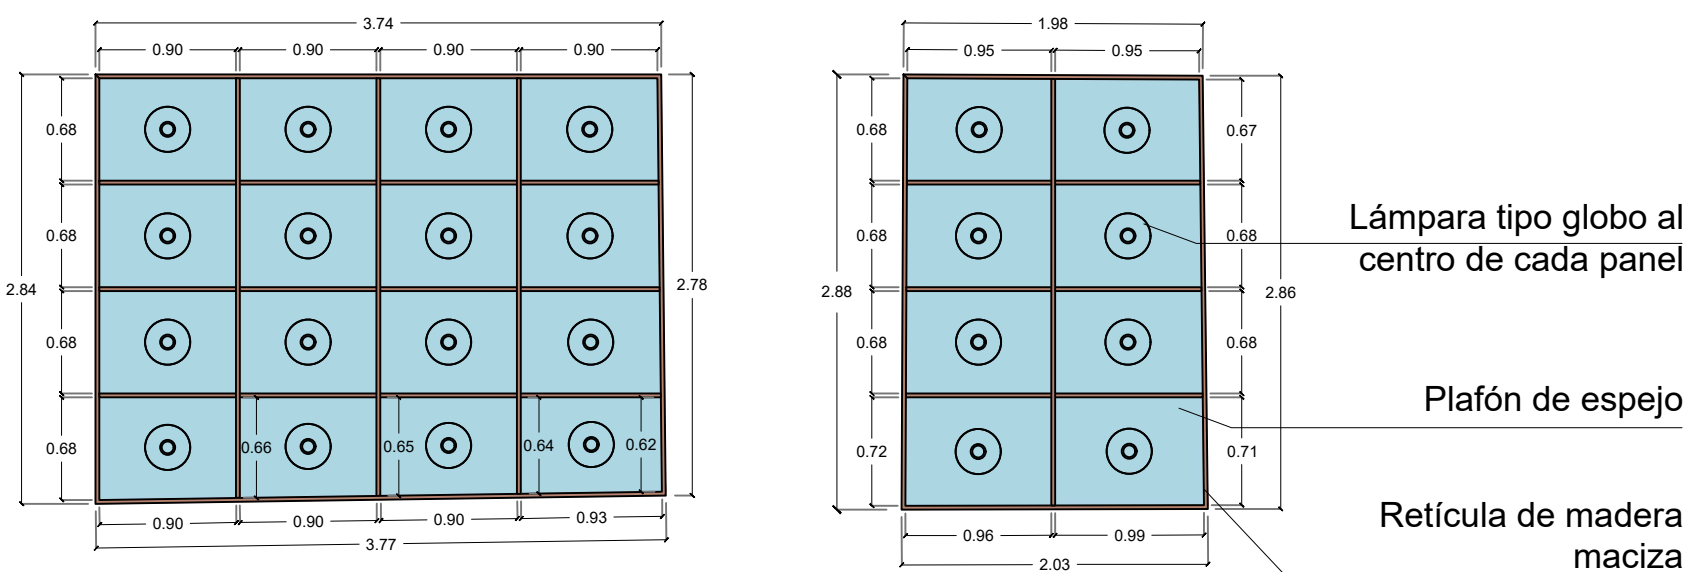

DET-01 PANELES DE ESPEJO


PASTICCIO

ESCALA 1:50

PLANTA BAJA DE ACABADOS EN PLAFONES CON DETALLES

PASTICCIO

ESCALA 1:75

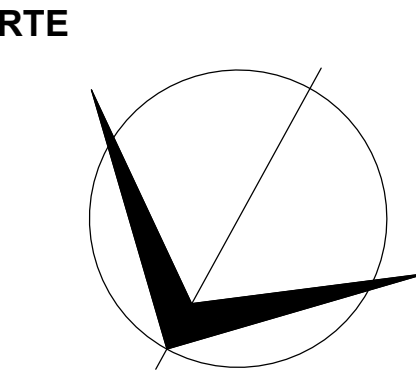

PROYECTO:

PASTICCIO

DOMICILIO:


Praga 33, colonia Juárez Ciudad de México, CDMX

NOTAS GENERALES:

- 1.- LAS COTAS RIGEN AL DIBUJO.
- 2.- LOS PLANOS ARQUITECTÓNICOS RIGEN SOBRE LOS PLANOS DE INGENIERÍAS Y/O ESTRUCTURALES. CUALQUIER DISCREPANCIA DEBERÁ CONSULTARSE CON EL ÁREA DE DISEÑO, Y SUSPENDER EL TRABAJO HASTA QUE LA SOLUCIÓN SEA APROBADA.
- 3.- ANTES DE INICIAR CUALQUIER TRABAJO, DEBERÁN VERIFICARSE EN OBRA LAS MEDIDAS Y NIVELES, SUJETÁNDOSE AL INCISO No. 2.
- 4.- EL CONTRATISTA ES RESPONSABLE DE TRABAJAR SIEMPRE CON UN JUEGO COMPLETO DE PLANOS. CUALQUIER DUDA EN LA INTERPRETACIÓN DE LOS MISMOS, DEBERÁ CONSULTARSE CON LA DIRECCIÓN DE OBRA Y EL ARQUITECTO.
- 5.- TODOS LOS NIVELES ARQUITECTÓNICOS SERÁN REFERIDOS A UN BANCO DE NIVEL DETERMINADO EN OBRA.

SIMBOLOGÍA:

NIVEL DE PISO TERMINADO

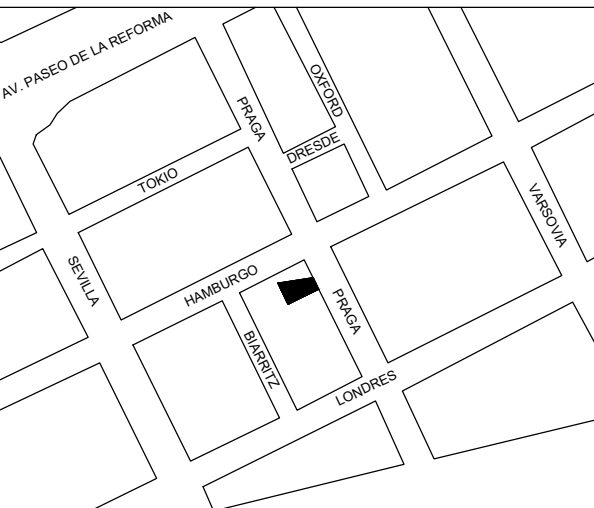

ÁREAS

PROPIETARIO:

DISEÑO:

MYTELVAK

Plano y V. Sec. Miguel Hidalgo CP 11960

TÍTULO:

PLANTA ALTA DE ACABADOS EN PLAFONES CON DETALLES

DIBUJÓ: IAP

REVISÓ:


FECHA: Noviembre 03, 2023

ACOTACIÓN: METROS

ESCALA: 1:75


CLAVE:

PLF.02

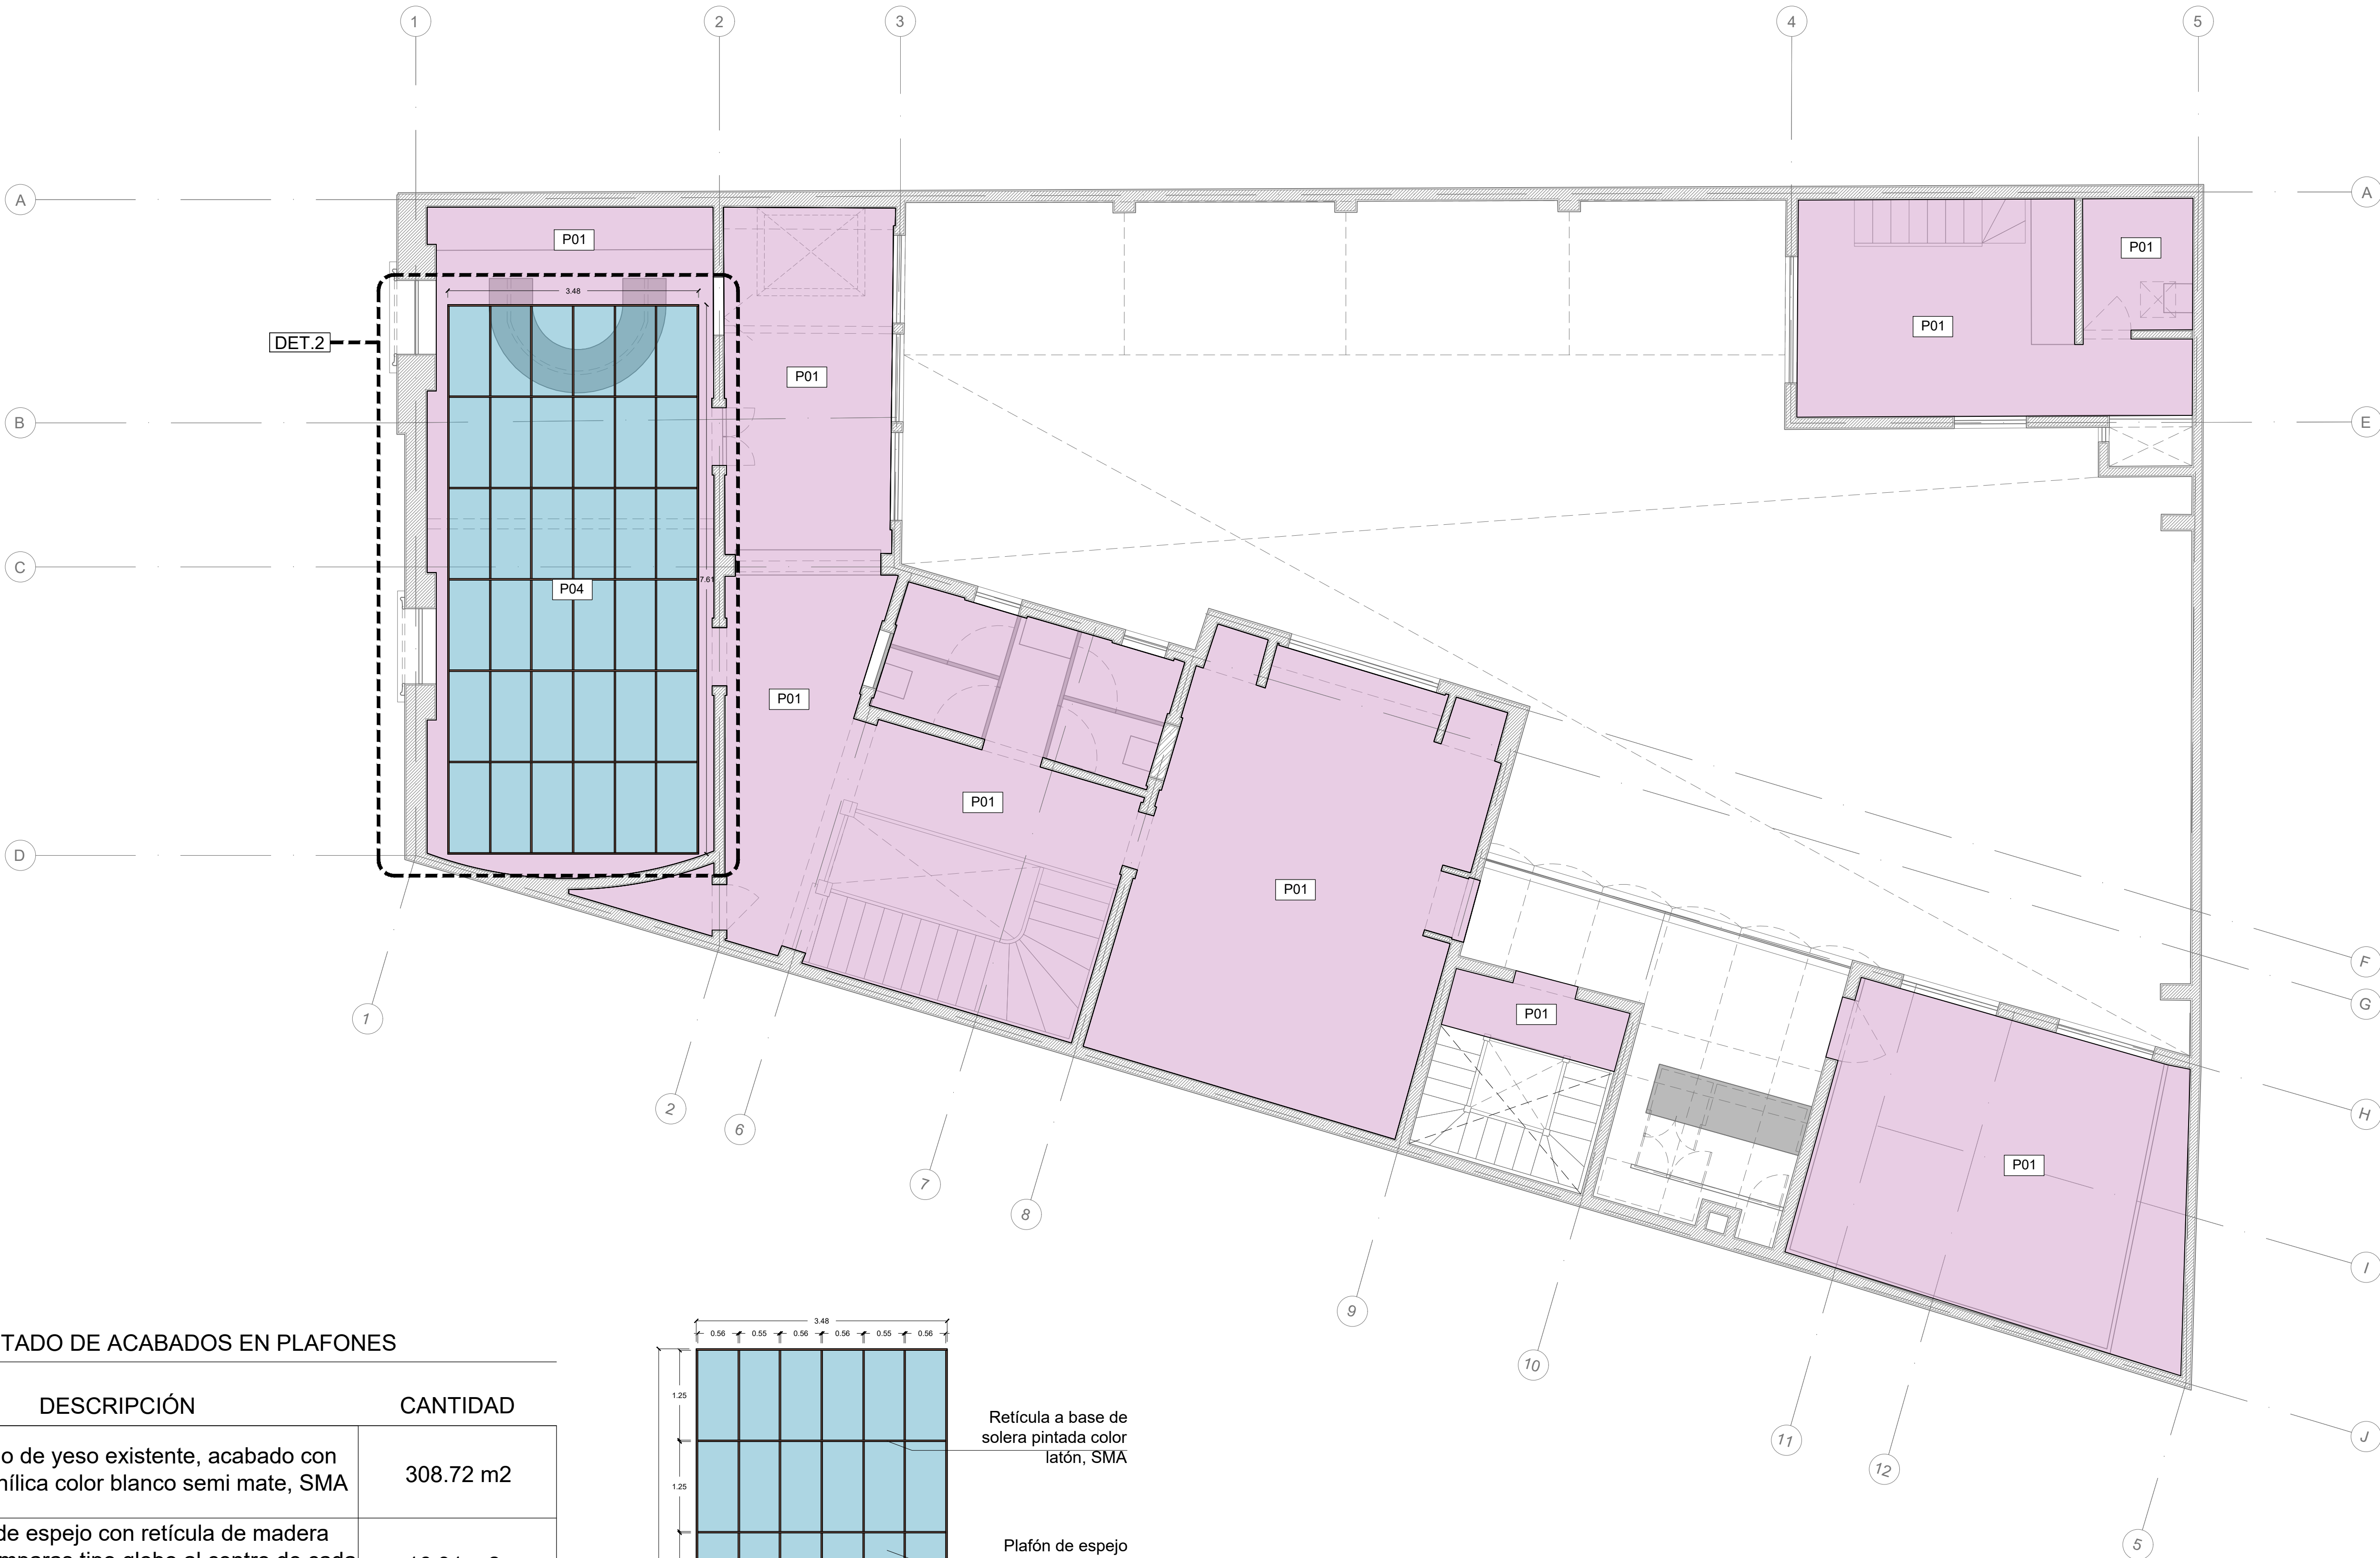

LISTADO DE ACABADOS EN PLAFONES

	DESCRIPCIÓN	CANTIDAD
P01	Aplanado de yeso existente, acabado con pintura vinílica color blanco semi mate, SMA	308.72 m2
P02	Plafón de espejo con retícula de madera maciza, lámparas tipo globo al centro de cada panel	16.31 m2
P03	Estructura para toldo con vegetación	31.76 m2
P04	Plafón de espejo con retícula a base de solera pintada color latón, SMA	26.45 m2

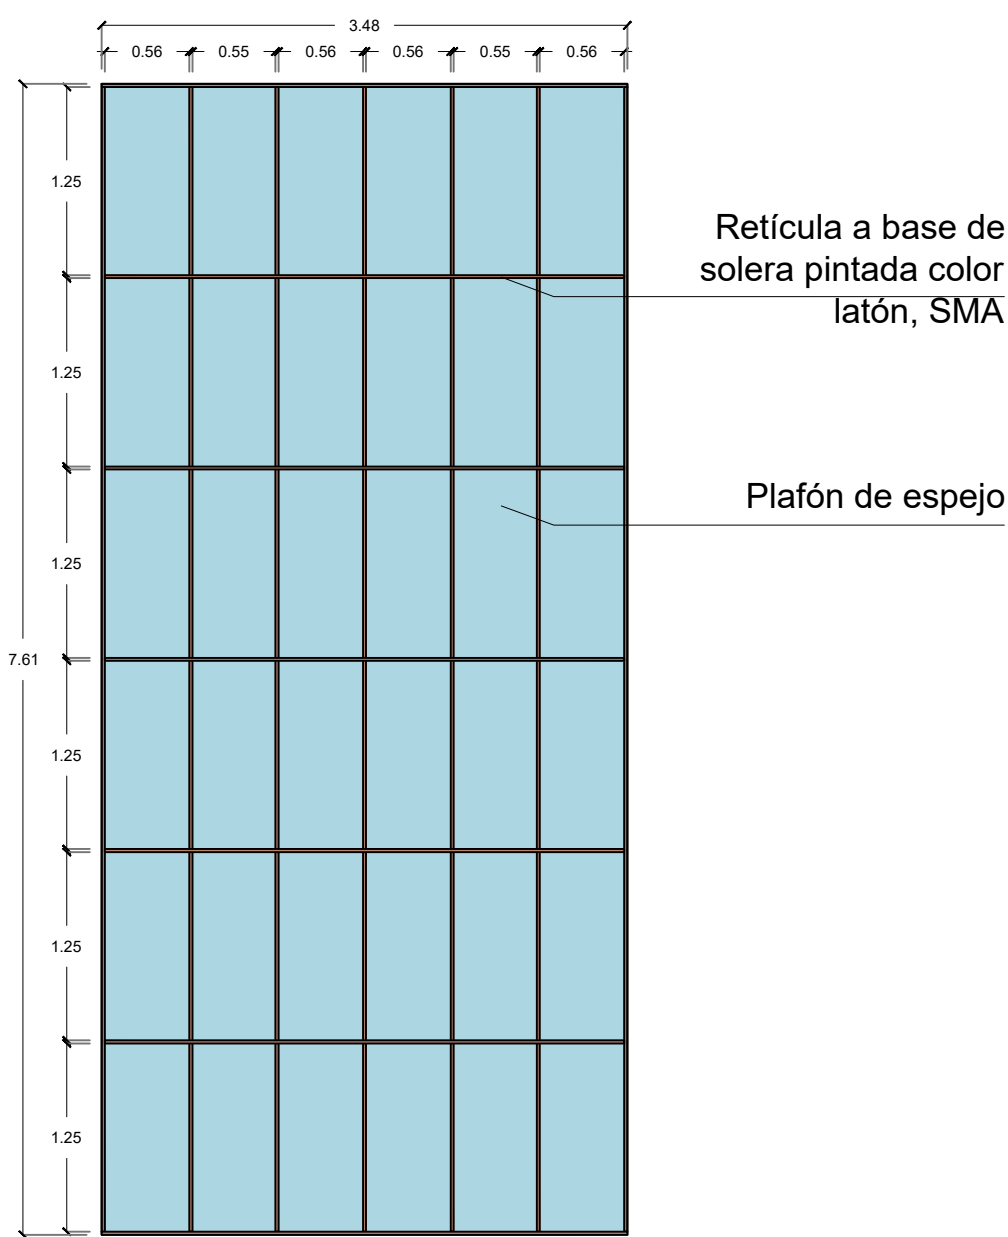

DET-02 PANELES DE ESPEJO


PASTICCIO

ESCALA 1:50

PLANTA ALTA DE ACABADOS EN PLAFONES CON DETALLES

PASTICCIO

ESCALA 1:75

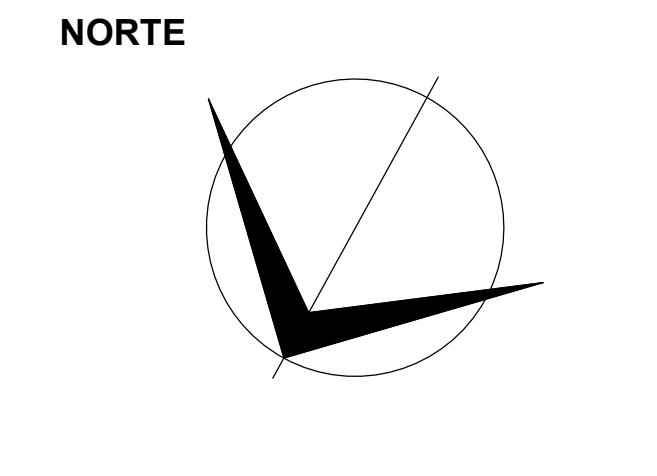

PROYECTO:

PASTICCIO


DOMICILIO:
Praga 33, colonia Juárez Ciudad de México, CDMX

NOTAS GENERALES:

- 1.- LAS COTAS RIGEN AL DIBUJO.
- 2.- LOS PLANOS ARQUITECTÓNICOS RIGEN SOBRE LOS PLANOS DE INGENIERÍAS Y/O ESTRUCTURALES, CUALQUIER DISCREPANCIA DEBERÁ CONSULTARSE CON EL ÁREA DE DISEÑO, Y SUSPENDER EL TRABAJO HASTA QUE LA SOLUCIÓN SEA APROBADA.
- 3.- ANTES DE INICIAR CUALQUIER TRABAJO, DEBERÁN VERIFICARSE EN OBRA LAS MEDIDAS Y NIVELES, SUJETÁNDOSE AL INCISO No. 2.
- 4.- EL CONTRATISTA ES RESPONSABLE DE TRABAJAR SIEMPRE CON UN JUEGO COMPLETO DE PLANOS, CUALQUIER DUDA EN LA INTERPRETACIÓN DE LOS MISMOS, DEBERÁ CONSULTARSE CON LA DIRECCIÓN DE OBRA Y EL ARQUITECTO.
- 5.- TODOS LOS NIVELES ARQUITECTÓNICOS SERÁN REFERIDOS A UN BANCO DE NIVEL DETERMINADO EN OBRA.

SIMBOLOGÍA:

NIVEL DE PISO TERMINADO

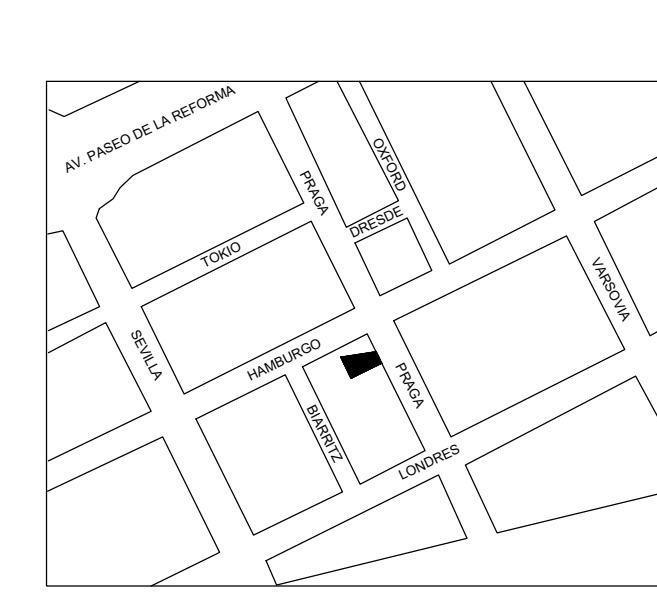

ÁREAS

PROPIETARIO:

DISEÑO:

MYTELVAK

Plano y Sec. Miguel Hórrigo CP 1150

TÍTULO:
PLANTA DE SEGUNDO NIVEL
DE ACABADOS EN PLAFONES
CON DETALLES

DIBUJÓ: **IAP** REVISÓ:

FECHA: **Noviembre 03, 2023**

ACOTACIÓN: METROS ESCALA: 1:75

CLAVE:

PLF.03




	DESCRIPCIÓN	CANTIDAD
P01	Aplanado de yeso existente, acabado con pintura vinílica color blanco semi mate, SMA	308.72 m2
P02	Plafón de espejo con retícula de madera maciza, lámparas tipo globo al centro de cada panel	16.31 m2
P03	Estructura para toldo con vegetación	31.76 m2
P04	Plafón de espejo con retícula a base de solera pintada color latón, SMA	26.45 m2

PLANTA DE SEGUNDO NIVEL DE ACABADOS EN PLAFONES CON DETALLES

PASTICCIO ESCALA 1:75

PASTICCIO ESCALA 1:75

NORTE

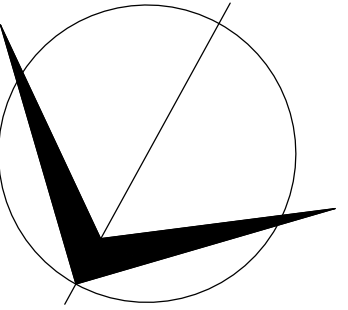

PROYECTO:

PASTICCIO

DOMICILIO:


Praga 33, colonia Juárez Ciudad de México, CDMX

NOTAS GENERALES:

- 1.- LAS COTAS RIGEN AL DIBUJO.
- 2.- LOS PLANOS ARQUITECTÓNICOS RIGEN SOBRE LOS PLANOS DE INGENIERÍAS Y/O ESTRUCTURALES. CUALQUIER DISCREPANCIA DEBERÁ CONSULTARSE CON EL ÁREA DE DISEÑO, Y SUSPENDER EL TRABAJO HASTA QUE LA SOLUCIÓN SEA APROBADA.
- 3.- ANTES DE INICIAR CUALQUIER TRABAJO, DEBERÁN VERIFICARSE EN OBRA LAS MEDIDAS Y NIVELES, SUJETÁNDOSE AL INCISO No. 2.
- 4.- EL CONTRATISTA ES RESPONSABLE DE TRABAJAR SIEMPRE CON UN JUEGO COMPLETO DE PLANOS. CUALQUIER DUDA EN LA INTERPRETACIÓN DE LOS MISMOS, DEBERÁ CONSULTARSE CON LA DIRECCIÓN DE OBRA Y EL ARQUITECTO.
- 5.- TODOS LOS NIVELES ARQUITECTÓNICOS SERÁN REFERIDOS A UN BANCO DE NIVEL DETERMINADO EN OBRA.

SIMBOLOGÍA:

NIVEL DE PISO TERMINADO

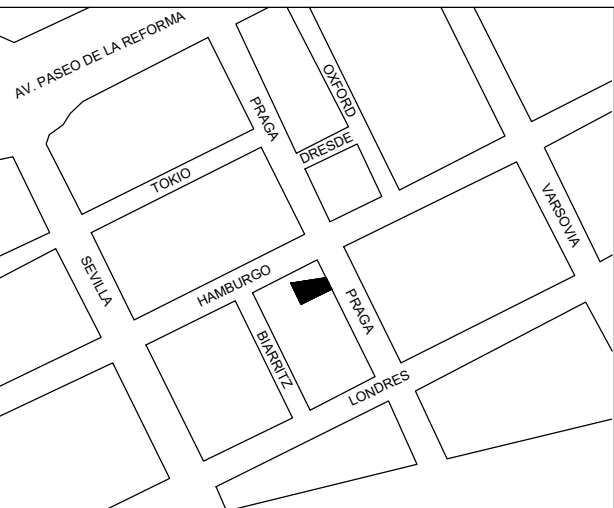

ÁREAS

PROPIETARIO:

DISEÑO:

MYTOLVOK

Plano V. Sec. Miguel Hidalgo CP 11960

TÍTULO:

PLANTA BAJA DE ACABADOS EN PISOS CON DETALLES

DIBUJÓ: IAP

REVISÓ:

FECHA: Noviembre 03, 2023

ACOTACIÓN: METROS

ESCALA: 1:75

CLAVE:

PIS.01

SIMBOLOGÍA PISOS			
CLAVE	SIMBOLOGÍA	TIPO	M2
P01		Acabado en piso en terrazo color gris, formato 20x20cm, existente	24
P02		Mantenimiento de duela de madera de pino de 19mm sobre bastidor de pino, existente	22.58
P03		Piso Kronos estructurado, color gris, formato 40cm x 40cm, marca Inter ceramic	4.38
P04		Piso de pasta, formato 20x20cm, acabado en ajedrez, colores amarillo y blanco	24
P05		Piso de pasta, formato 20x20cm, acabado en ajedrez, colores rojo y blanco	87.76
P06		Estructura de bastidor de herrería para recibir deck de madera de 12cm de altura	63.24
P06		Acabado de grava blanca con huellas de piedra, SMA	54.34



INDICA CAMBIO DE PISO



INDICA ACABADO EN PISOS

PLANTA BAJA DE ACABADOS EN PISOS CON DETALLES

PASTICCIO

ESCALA 1:75



PASTICCIO

Praga 33, colonia Juárez Ciudad de México, CDMX

1.- LAS COTAS RIGEN AL DIBUJO.

2.- LOS PLANOS ARQUITECTÓNICOS RIGEN SOBRE LOS PLANOS DE INGENIERÍAS Y/O ESTRUCTURALES, CUALQUIER DISCREPANCIA DEBERÁ CONSULTARSE CON EL ÁREA DE DISEÑO, Y SUSPENDER EL TRABAJO HASTA QUE LA SOLUCIÓN SEA APROBADA.

3.- ANTES DE INICIAR CUALQUIER TRABAJO, DEBERÁN VERIFICARSE EN OBRA LAS MEDIDAS Y NIVELES, SUJETÁNDOSE AL INCISO No. 2.

4.- EL CONTRATISTA ES RESPONSABLE DE TRABAJAR SIEMPRE CON UN JUEGO COMPLETO DE PLANOS. CUALQUIER DUDA EN INTERPRETACIÓN DE LOS MISMOS, DEBERÁ CONSULTARSE CON LA DIRECCIÓN DE OBRA Y ARQUITECTO.

5.- TODOS LOS NIVELES ARQUITECTÓNICOS
SERÁN REFERIDOS A UN BANCO DE NIVEL
DETERMINADO EN OBRA.

NIVEL DE PISO TERMINADO



DISEÑO:

Polanco V. Seco, Miguel Hidalgo CP 1150

DIBUJÓ: IAP

REVISÓ:

FECHA: **Noviembre 03, 2023**

ACOTACIÓN: METROS

ESCALA: 1:75

CLAVE:

PIS.02




 INDICA CAMBIO DE PISO

P 01 INDICA ACABADO EN PISOS

PLANTA ALTA DE ACABADOS EN PISOS CON DETALLES

PASTICCIO

ESCALA 1:75

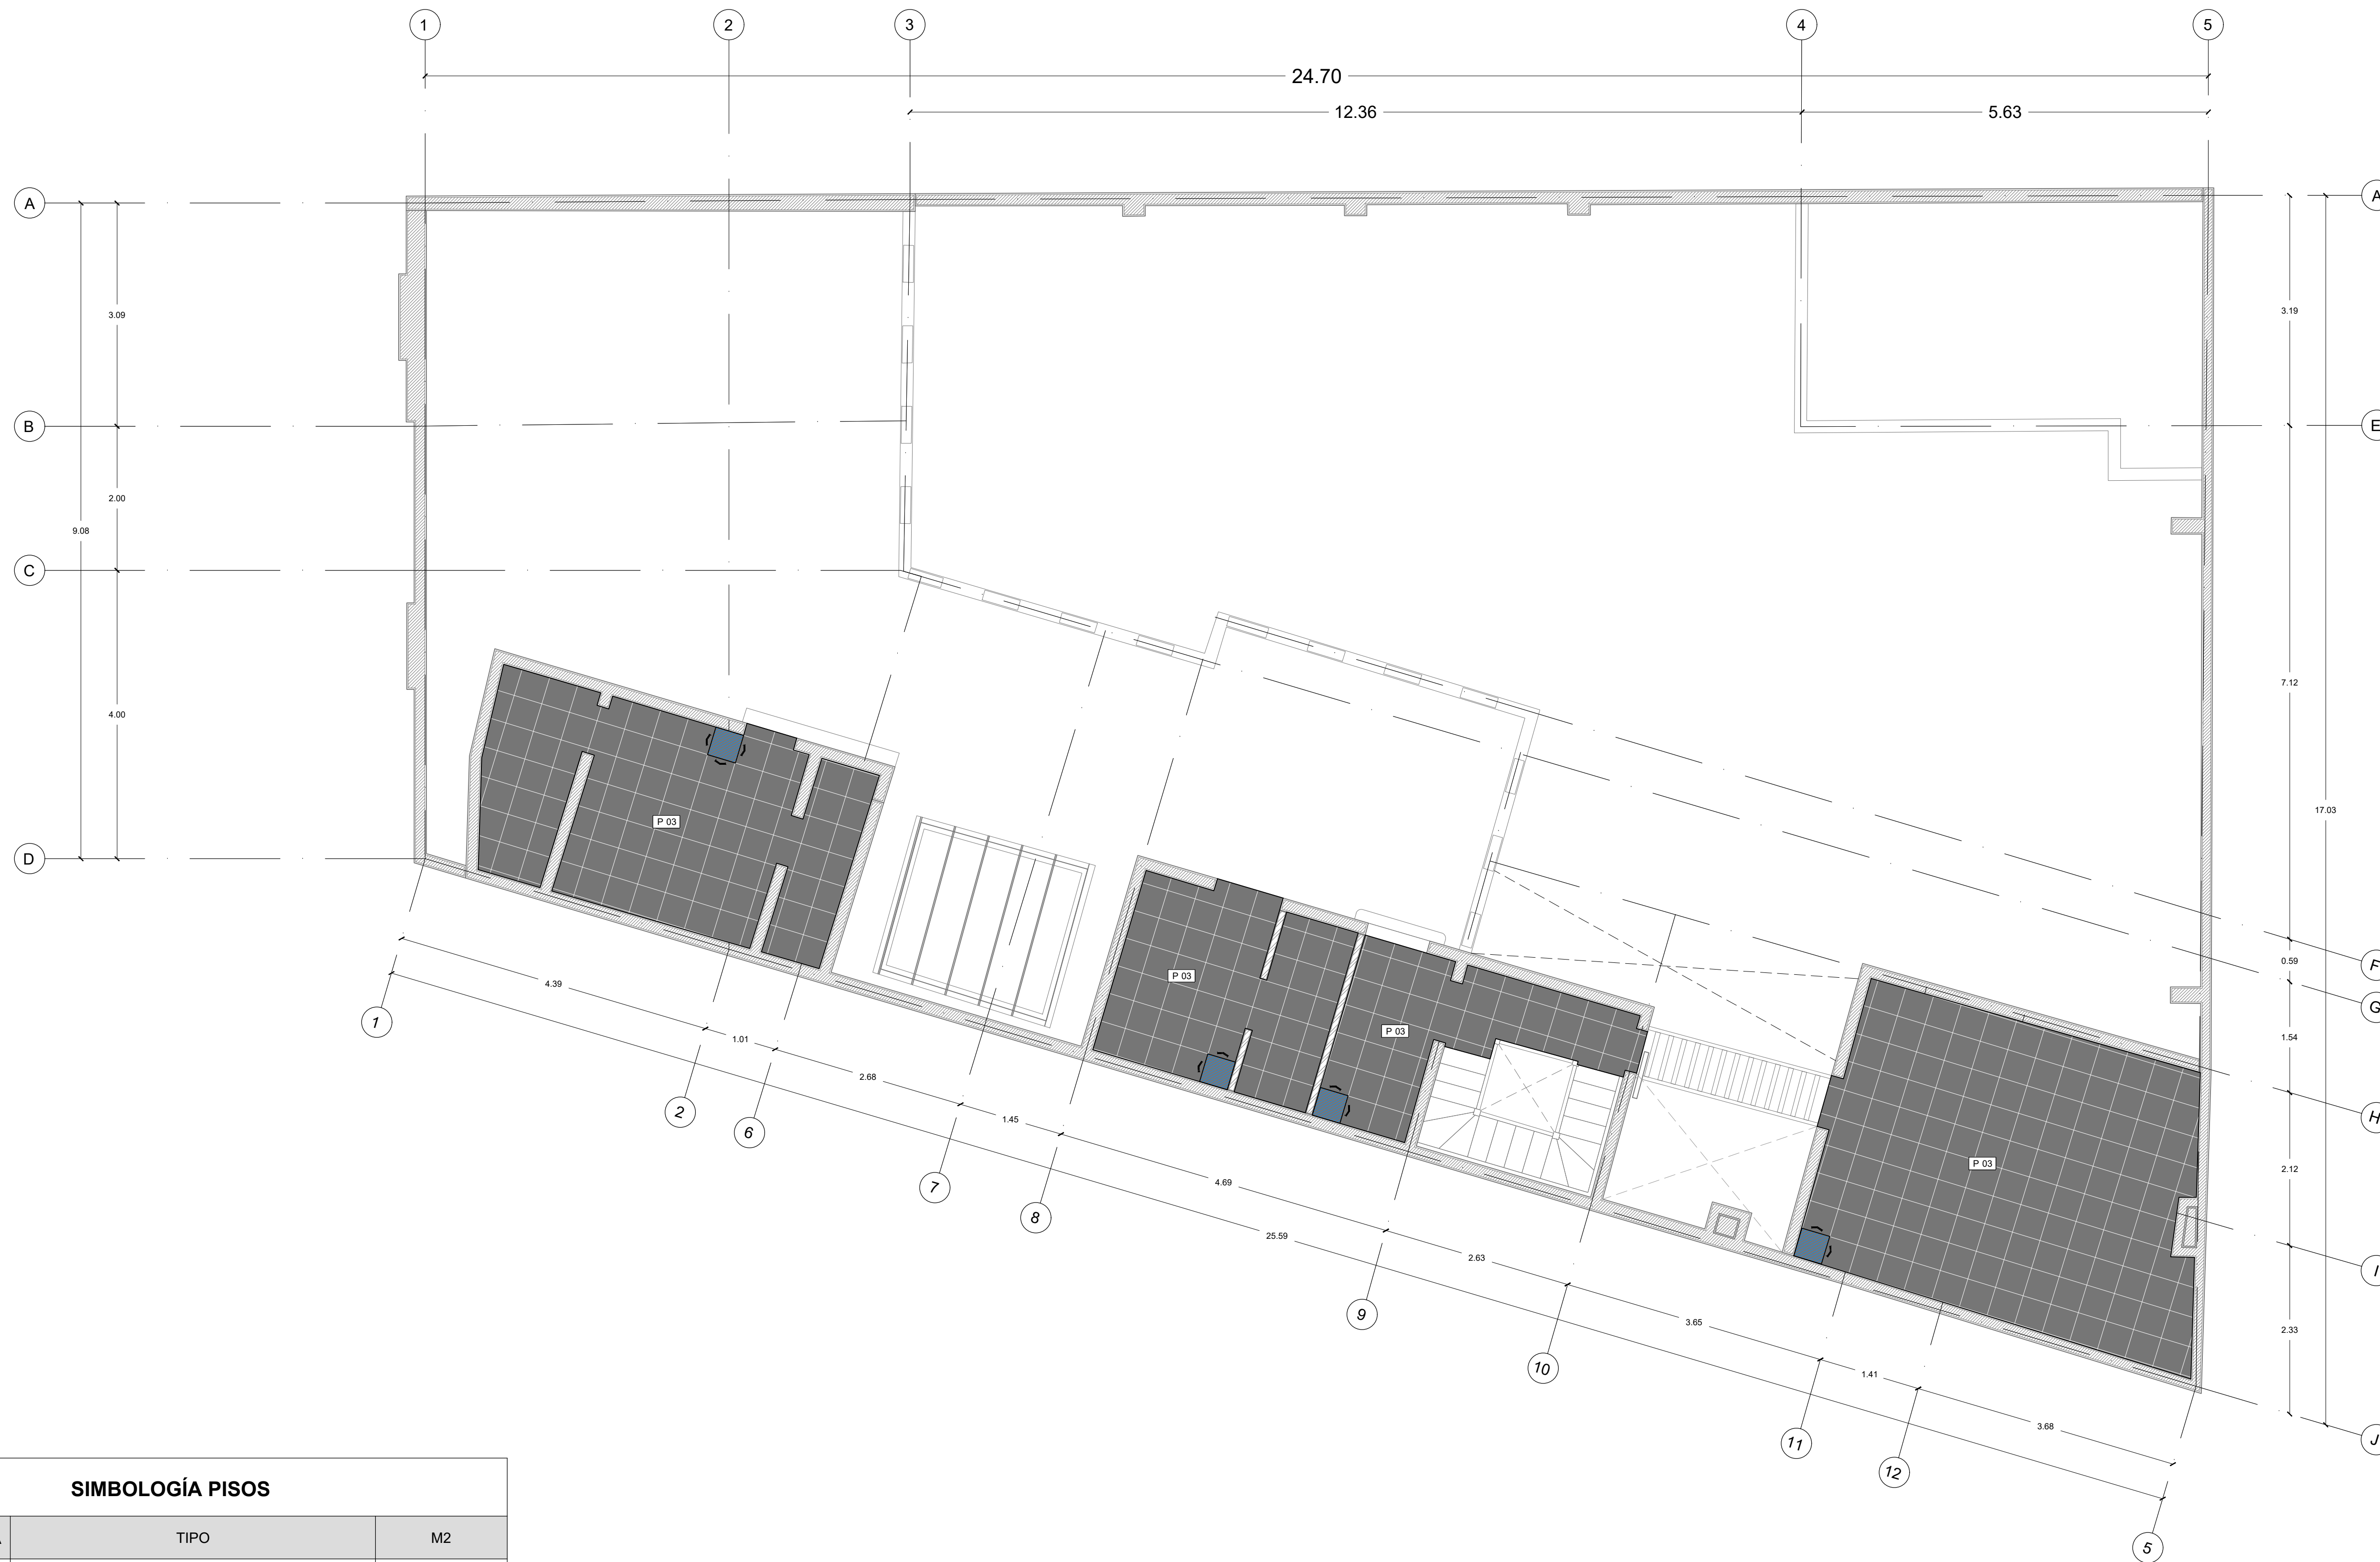


SIMBOLOGÍA PISOS			
CLAVE	SIMBOLOGÍA	TIPO	M2
P03		Piso Kronos estructurado, color gris, formato 40cm x 40cm, marca Inter ceramic	49.28

- INDICA CAMBIO DE PISO
- INDICA ACABADO EN PISOS

PLANTA DE SEGUNDO NIVEL DE ACABADOS EN PISOS CON DETALLES
PASTICCIO
ESCALA 1:75

NORTE

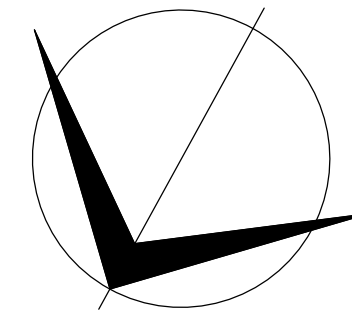

PROYECTO:

PASTICCIO

DOMICILIO:


Praga 33, colonia Juárez Ciudad de México, CDMX

NOTAS GENERALES:

- 1.- LAS COTAS RIGEN AL DIBUJO.
- 2.- LOS PLANOS ARQUITECTÓNICOS RIGEN SOBRE LOS PLANOS DE INGENIERÍAS Y/O ESTRUCTURALES. CUALQUIER DISCREPANCIA DEBERÁ CONSULTARSE CON EL ÁREA DE DISEÑO, Y SUSPENDER EL TRABAJO HASTA QUE LA SOLUCIÓN SEA APROBADA.
- 3.- ANTES DE INICIAR CUALQUIER TRABAJO, DEBERÁN VERIFICARSE EN OBRA LAS MEDIDAS Y NIVELES, SUJETÁNDOSE AL INCISO No. 2.
- 4.- EL CONTRATISTA ES RESPONSABLE DE TRABAJAR SIEMPRE CON UN JUEGO COMPLETO DE PLANOS. CUALQUIER DUDA EN LA INTERPRETACIÓN DE LOS MISMOS, DEBERÁ CONSULTARSE CON LA DIRECCIÓN DE OBRA Y EL ARQUITECTO.
- 5.- TODOS LOS NIVELES ARQUITECTÓNICOS SERÁN REFERIDOS A UN BANCO DE NIVEL DETERMINADO EN OBRA.

SIMBOLOGÍA:

NIVEL DE PISO TERMINADO

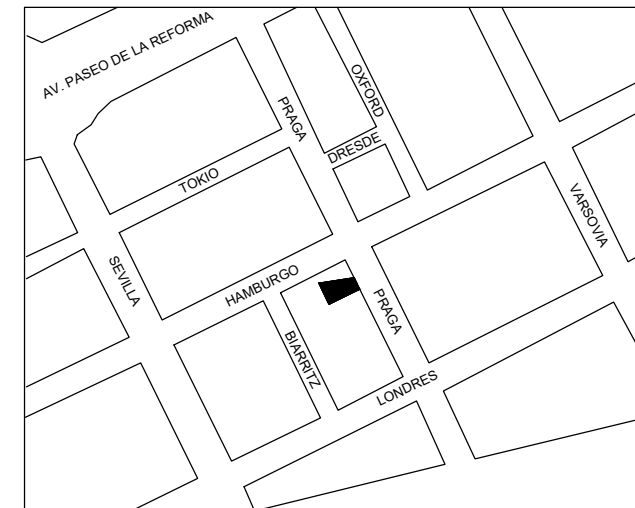

ÁREAS

PROPIETARIO:

DISEÑO:

MYTELVAK

Plano V. Sec. Miguel Hidalgo CP 11960

TÍTULO:

PLANTA DE SEGUNDO NIVEL
DE ACABADOS EN PISOS CON
DETALLES

DIBUJÓ: IAP

REVISÓ:

FECHA: Noviembre 03, 2023

ACOTACIÓN: METROS

ESCALA: 1:75

CLAVE:

PIS.03