

CROQUIS DE LOCALIZACIÓN:

DIRECCIÓN:
Praga 33, colonia Juárez
Ciudad de México, CDMX

CONTENIDO:

PLANTA
ARQUITECTONICA

NOTAS:

1. VERIFICAR LAS MEDIDAS Y VOLUMENES EN EL CASO DE DIVERGENCIAS ENTRE EL PLANO ARQUITECTÓNICO Y EL ESTRUCTURAL, PASE LOS ARQUITECTOS A PRIMA CONSULTA CON EL ESTRUCTURAL.
2. LAS ACOTACIONES PRECEDERÁN SIEMPRE A LOS DIBUJOS.
3. CONCRETO C-150 PARA LOS PISOS Y EL DRENTO EN PLANTILLA QUE SERÁ CONCRETO F-150 K10CM.
4. REFORZO Y ACEROS PARA EL DRENTO DEL QUE SERÁ HIERRO CORROSADO.
5. LOS BAJOS DE DESPLAZAMIENTO DEL FONDO DE CONSTRUCCIÓN ANCLARÁN EL ACERO DE REFORZO LA LONGITUD "L".
6. LOS ANCLAJES Y TRABAJOS DE HERRAJE DE LA CONSTRUCCIÓN "L".
7. LOS DETALLES DE HERRAJE DE LA PLANTA Y EL FONDO DE CONSTRUCCIÓN.
8. NO SE PERMITE TRANSAPARAR MÁS DE 50% DEL ÁREA DE ACERO EN UNA MISMA SECCIÓN.
9. EL REFORZAMIENTO SERÁ DE 5 CM AL PISO DE LA VARELLA COMO LA SUPERFICIE DE DESPLAZAMIENTO EN CONTACTO CON PLANTILLA O TERRENO Y DE 3 CM EN TODO LO DEMÁS.
10. ACEROS ESTRUCTURALES: 2008 Y 2009.
11. DE CUBIERTA ESTRUCTURAL AL AL ACEROS DE 1008 Y 2009.
12. LA SOLDADURA DEBEN SER ELEGIDA POR PERSONAL CALIFICADO Y CUMPLIR CON LAS ESPECIFICACIONES DEL MANUAL DE CONSTRUCCIÓN DE ACERO (M.A.C.).
13. TODA LA ESTRUCTURA METALICA DEBEN APROTEGERSE CON DOS MANOS DE PINTURA ANTICORROSIÓN.


PALILLERIA

ELABORÓ:
DIDANF ARQUITECTURA TEXTIL

VERIFICÓ:
DIDANF ARQUITECTURA TEXTIL

CLIENTE:

PLANO:

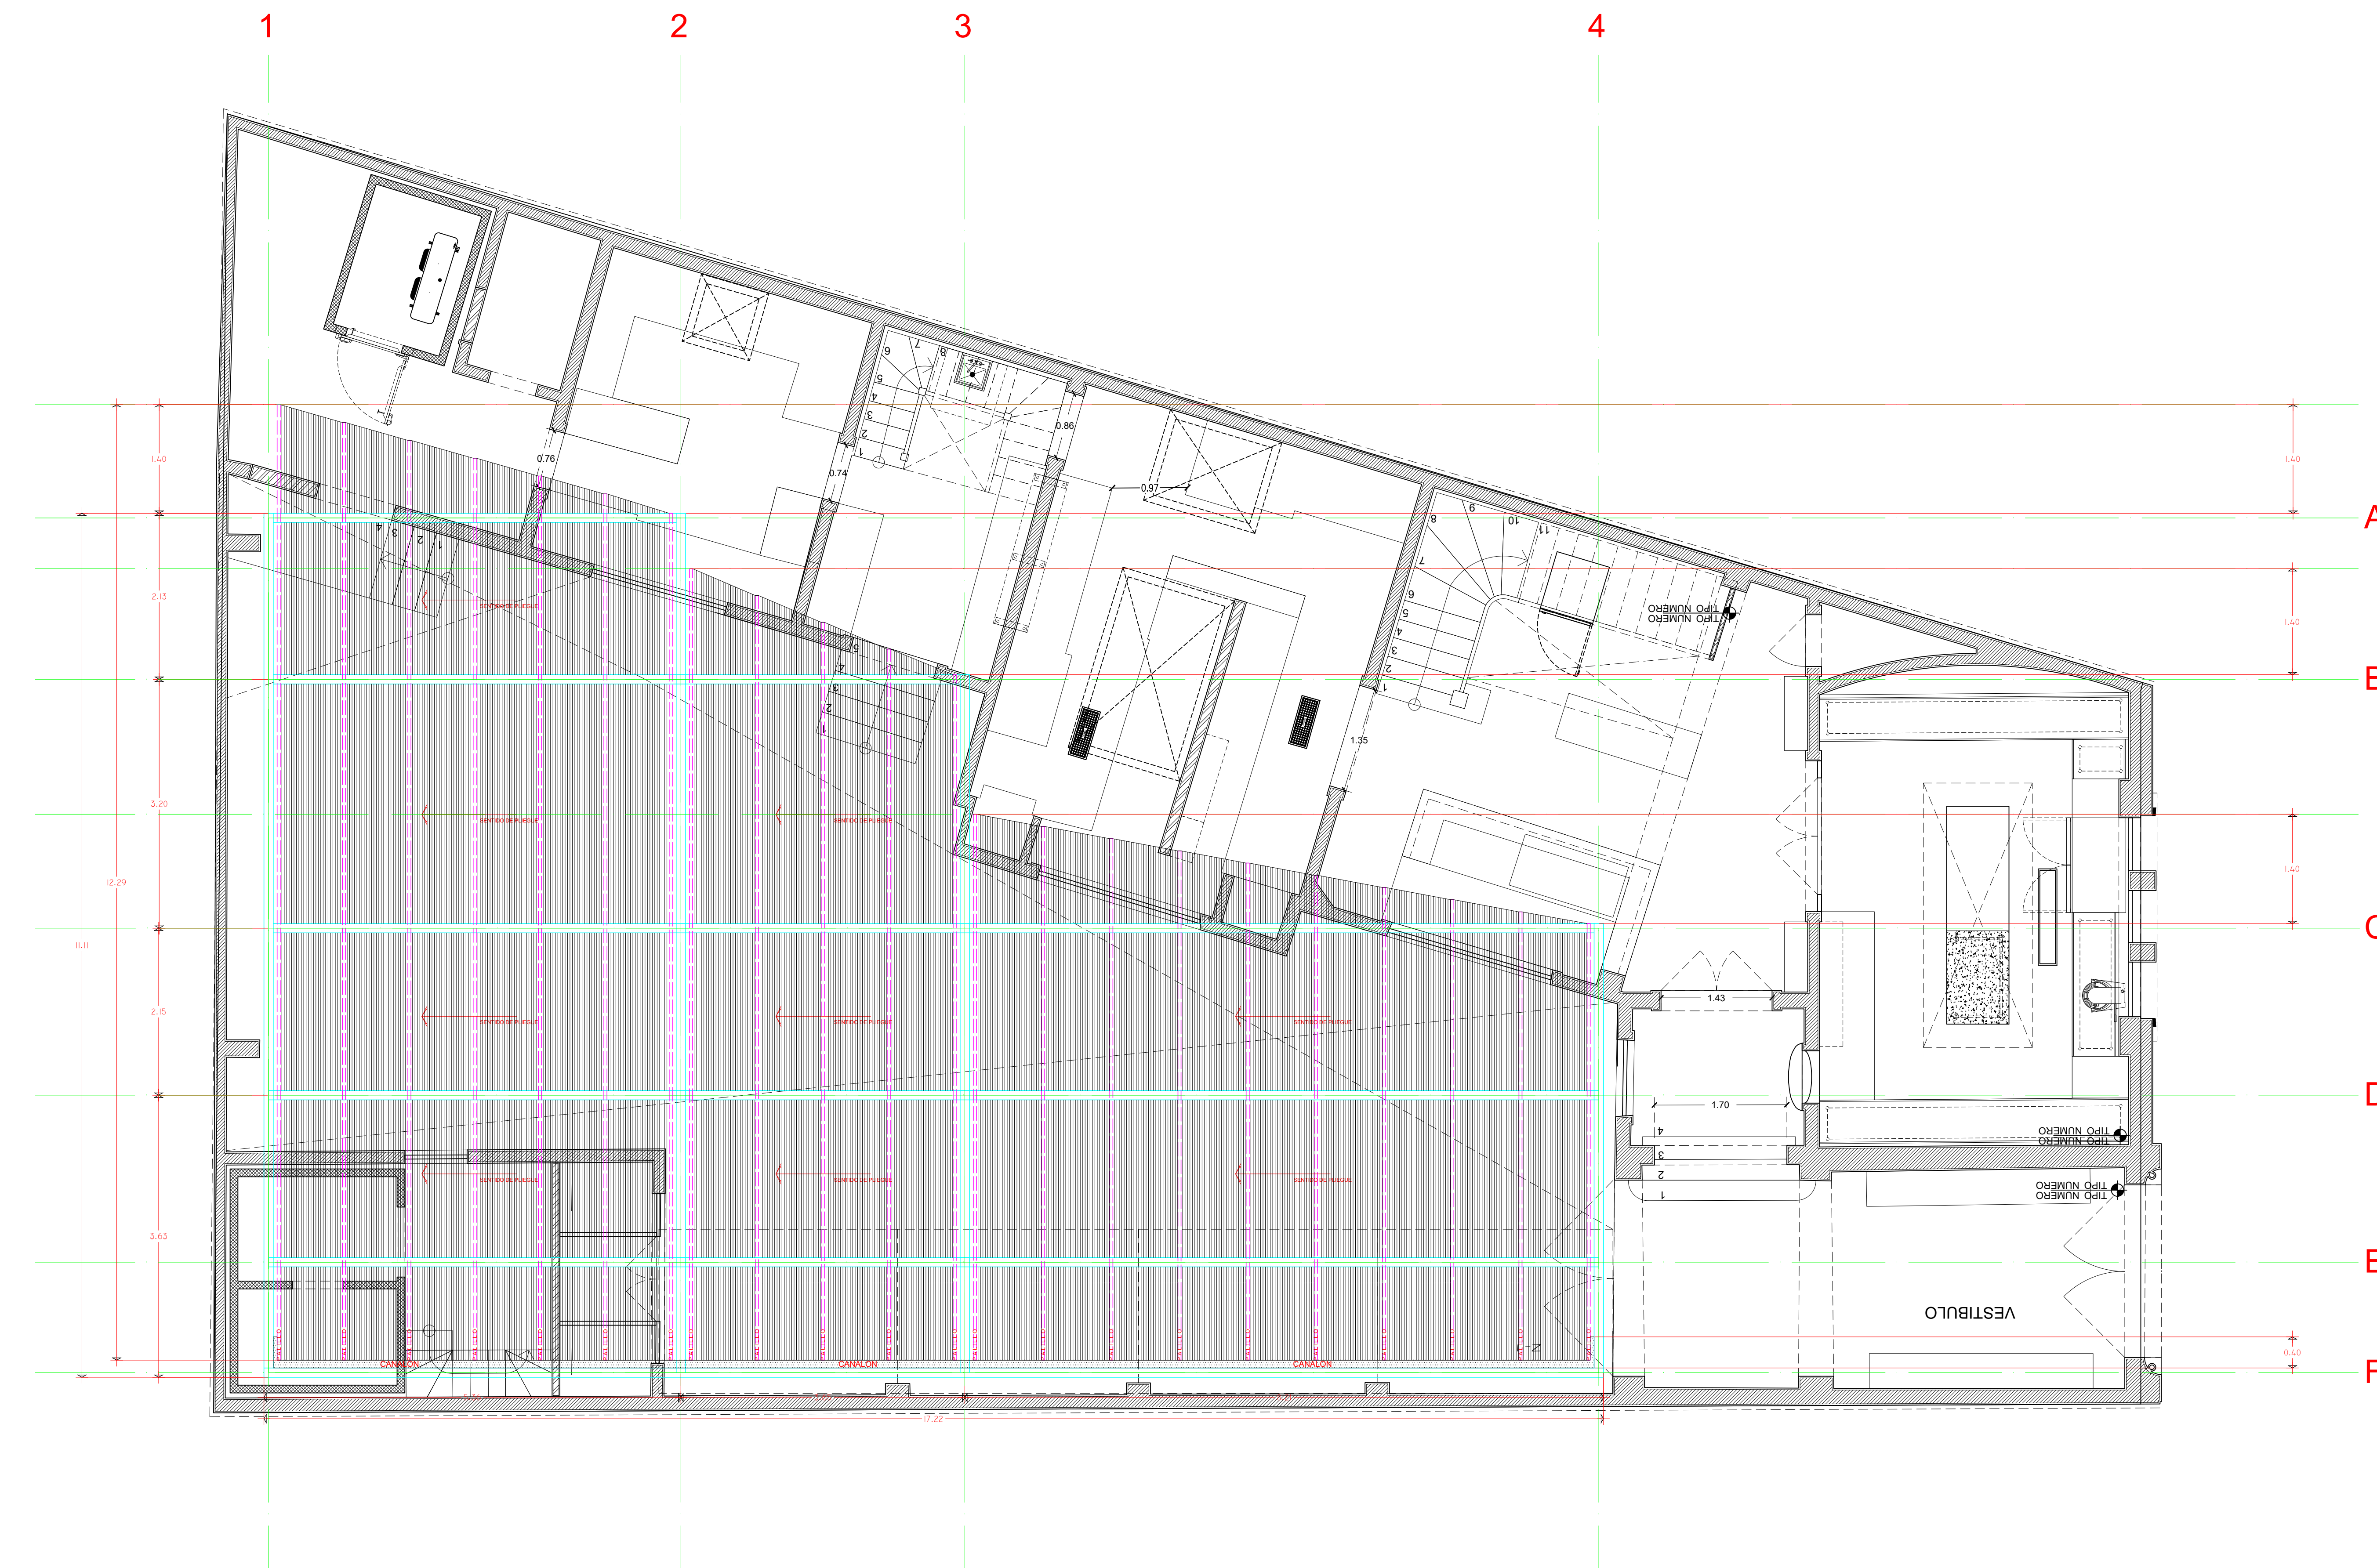

PLANTA

ARQUITECTONICA
DESPLEGADA